EMERGENCY ESCAPE & EVACUATION ROUTE LAYOUT

NOTES :

DRAWING REFERENCE	DESCRIPTION	REV	DATE	DESCRIPTION	PREPR'D	CHECK'D	APRV'D	CHECKED	APPROVED
TMBP-SP001-PI-PLP—101	OVERALL PLOT PLAN DRAWING (Rev-1)	A	17-12-2025	ISSUED FOR REVIEW	DDS	AS	RTN		

PT. PERTAMINA EP APPROVAL

PROCET :
JASA PEMBANGUNAN FASILITAS PRODUKSI STASIUN PENGUMPUL (SP) TANJUNG MIRING BARAT & KARANGAN TIMUR

OWNER : skkmigas, PERTAMINA EP

CONTRACTOR : POG

SCALE :	DRAWING NO.	SHEET. NO.	REV
NTS	TMBP – SP001 – PS – LAY – D103	01 OF 02	A

DRAWING TITLE :
EMERGENCY ESCAPE & EVACUATION ROUTE LAYOUT

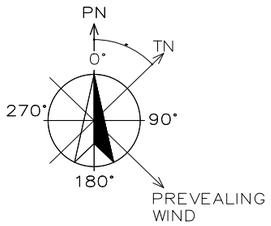

EQUIPMENT LIST				EQUIPMENT LIST			
NO	TAG. NO.	DESCRIPTION	GIRD	NO	TAG. NO.	DESCRIPTION	GIRD
1	PN-003	FIRE WATER POND	C2	22	V-007	CLOSED DRAIN VESSEL	C6
2	P-050A/B	VERTICAL FIRE WATER PUMP	C2	23	FL-001	FLARE STACK	C9
3	P-051	JOCKEY PUMP	C2	24	P-016AB,P-017AB,PN-002	SERVICE WATER	D7
4	Z-009	MANIFOLD CHEMICAL INJECTION	D4	25	T-003	TEST TANK TMB	E4
5	PN-001	SUMP PIT	C4	26	T-004	TEST TANK KRG	D4
6	P-002A	TEST PUMP TMB	D5	27	T-006B	STORAGE TANK KRG	C6
7	P-003A/B	TEST PUMP KRG	D5	28	T-005A	STORAGE TANK TMB	D5
8	P-001A/B	GROSS TRANSFER PUMP	C5	29	T-005B	STORAGE TANK TMB	D5
9	V-001	PROD. SEPARATOR TMB	E4	30	T-006A (EXISTING)	STORAGE TANK KRG (EXISTING)	C5
10	V-002	PROD. SEPARATOR KRG	E4	31	P-006A/B	KOD PUMP	D6
11	V-003	TEST SEPARATOR TMB	E4	32	P-007A/B	CLOSED DRAIN PUMP	D6
12	V-004	TEST SEPARATOR KRG	E4	33	P-018	CLOSE DRAIN SUMP PUMP	D6
13	V-005	PROD. SCRUBBER	E4	34	P-019	WATER SUMP PUMP	C4
14	–	CONTROL ROOM	E6	35	P-016A/B	BOSTER PUMP	E7
15	–	WAREHOUSE & WORKSHOP	C6	36	P-017A/B	WATER DISTRIBUTION PUMP	D7
16	Z-002	FUEL GAS PACKAGE	E6	37	P-021	KOD SUMP PUMP	D6
17	GEG-001	GAS ENGINE GENERATOR	D6	38	T-019	DIESEL STORAGE TANK	E6
18	GEG-002	GAS ENGINE GENERATOR	D6	39	T-017	PORTABLE WATER TANK	D7
19	DEG-001	DIESEL ENGINE GENERATOR	D6	40	Z-004	WATER TREATMENT PACKAGE	D7
20	Z-005,V-009,V-010	IA/PA PACKAGE	E7	41	PN-002	WATER POND	E7
21	V-006	KNOCK OUT DRUM VESSEL	D6	42	P-008A/B	DEEP WELL PUMP	E4
				43	P-023	GROSS SUMP PUMP	C5
				44	P-040	STORAGE TANK SUMP PUMP	C5

LEGEND & SYMBOL

NO	SYMBOL	DESCRIPTION	QTY.
1		SAFETY SIGN: PRIMARY MUSTER POINT	1
2		SAFETY SIGN: SECONDARY MUSTER POINT	1
3		SAFETY SIGN: DRY CHEMICAL PORTABLE FIRE EXTINGUISHER	22
4		SAFETY SIGN: PORTABLE CO2 FIRE EXTINGUISHER	5
5		SAFETY SIGN: SAFETY SHOWER AND EYEWASH STATION	1
6		SAFETY SIGN: PORTABLE EYEWASH STATION	1
7		SAFETY SIGN: HIGH NOISE AREA & HEARING PROTECTION MANDATORY	3
8		SAFETY SIGN: CHEMICAL STORAGE AREA FOR AUTHORIZED PERSONNEL	2
9		SAFETY SIGN: FIRST AID KIT	2
10		SAFETY SIGN: EXIT (RIGHT SIGN)	9
11		SAFETY SIGN: (LEFT SIGN)	4
12		SAFETY SIGN: PRE REQUIRED	5
13		SAFETY SIGN: NO SMOKING AREA	5

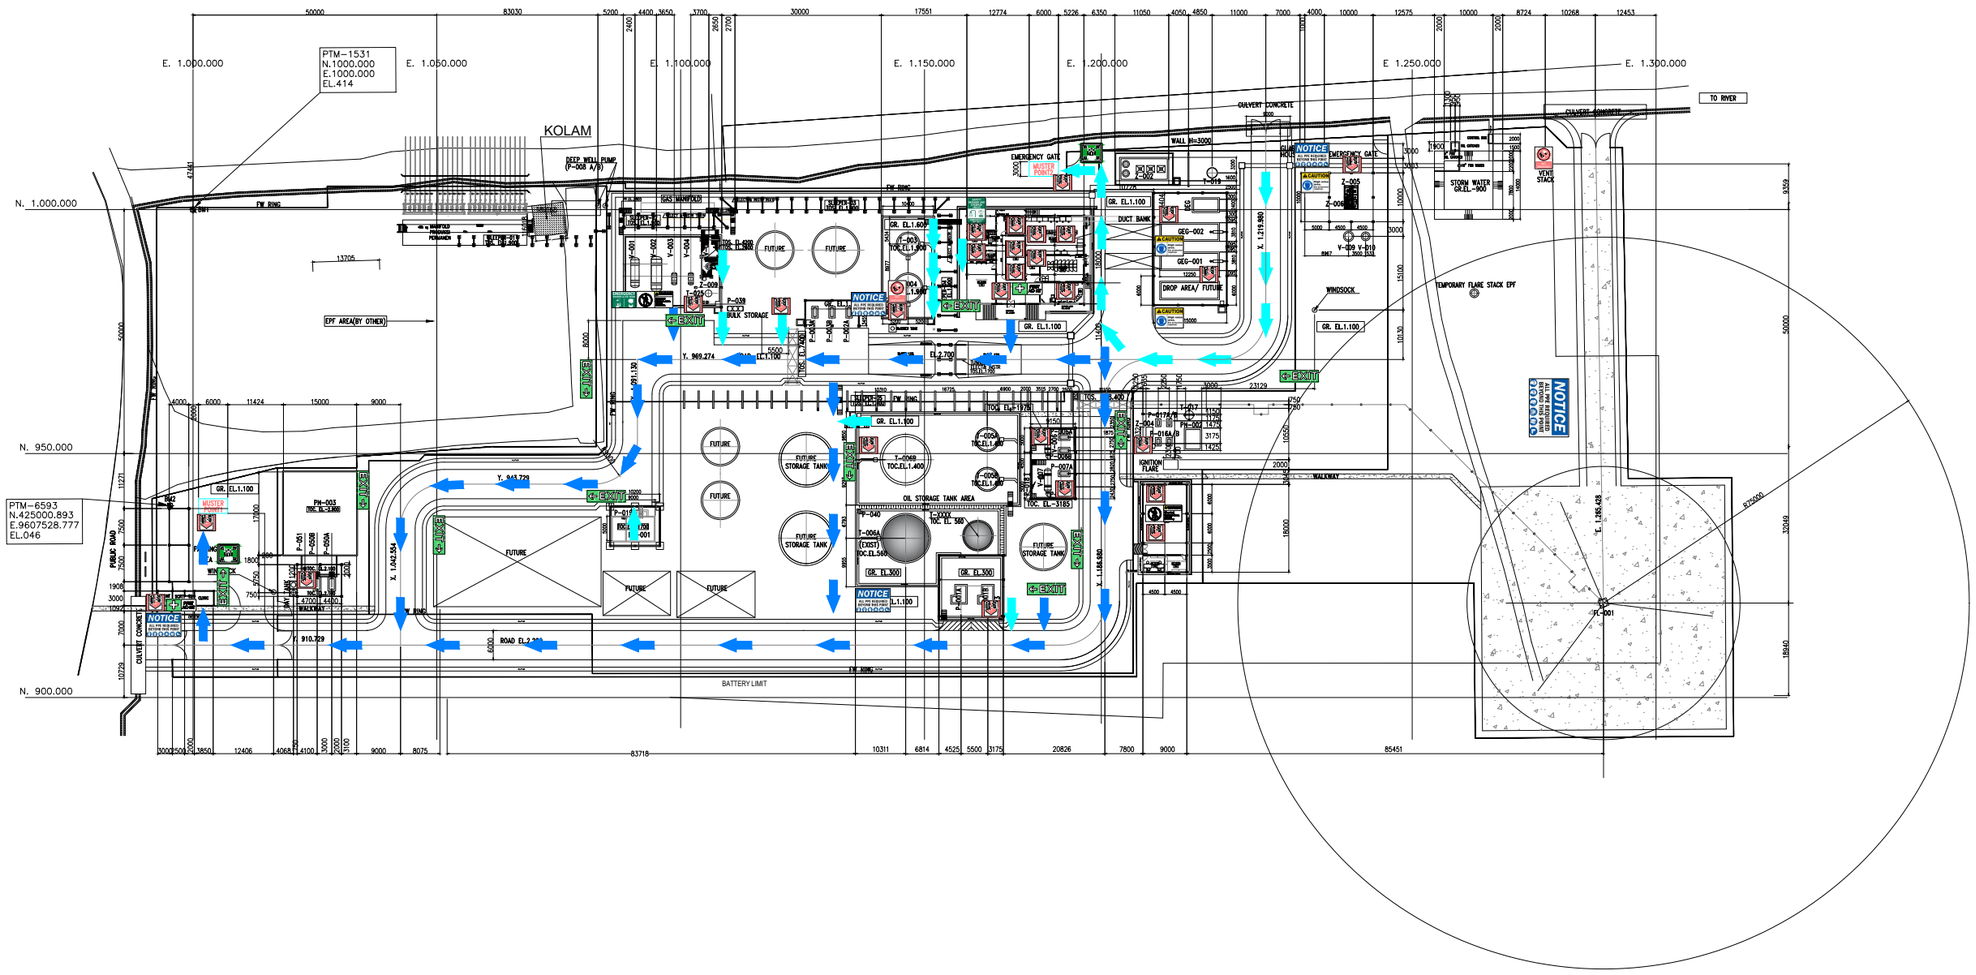

NO	LEGEND	DESCRIPTION
1		PRIMARY ESCAPE ROUTE
2		SECONDARY ESCAPE ROUTE
3	MUSTER POINT1	PRIMARY MUSTER POINT
4	MUSTER POINT2	SECONDARY MUSTER POINT

SIMBOL & KETERANGAN :

- BM / Patok Pilar
- Pagar Beton
- Pagar Harmonika
- Bangunan
- Kolam
- Pipa
- Jalan
- Sungai
- Rawa
- Kontur dan Label
- Jalan Existing
- Saluran Drainase

NOTES :

1. THE PRIMARY ESCAPE ROUTE SHALL BE MINIMUM 1.2 M OF WIDE AND 2.3 OF HEIGHT CLEARANCE.
2. THE SECONDAY ESCAPE ROUTE SHALL BE MINIMUM 0.5 M OF THE WIDE AND 2.3 OF HEIGHT CLEARANCE.

DRAWING REFERENCE	DESCRIPTION	REV	DATE	DESCRIPTION	PREPR'D	CHECK'D	APRV'D
TMBP-SP001-PI-PLP-101	OVERALL PLOT PLAN DRAWING (Rev-1)	A	17-12-2025	ISSUED FOR REVIEW	DDS	AS	RTN

PT. PERTAMINA EP APPROVAL

CHECKED | APPROVED

PROCET :
JASA PEMBANGUNAN FASILITAS PRODUKSI STASIUN PENGUMPUL (SP) TANJUNG MIRING BARAT & KARANGAN TIMUR

OWNER : skkmigas PERTAMINA EP

CONTRACTOR : POG

SCALE :	DRAWING NO.	SHEET. NO.	REV
NTS	TMBP – SP001 – PS – LAY – D103	02 OF 02	A

DRAWING TITLE :
EMERGENCY ESCAPE & EVACUATION ROUTE LAYOUT