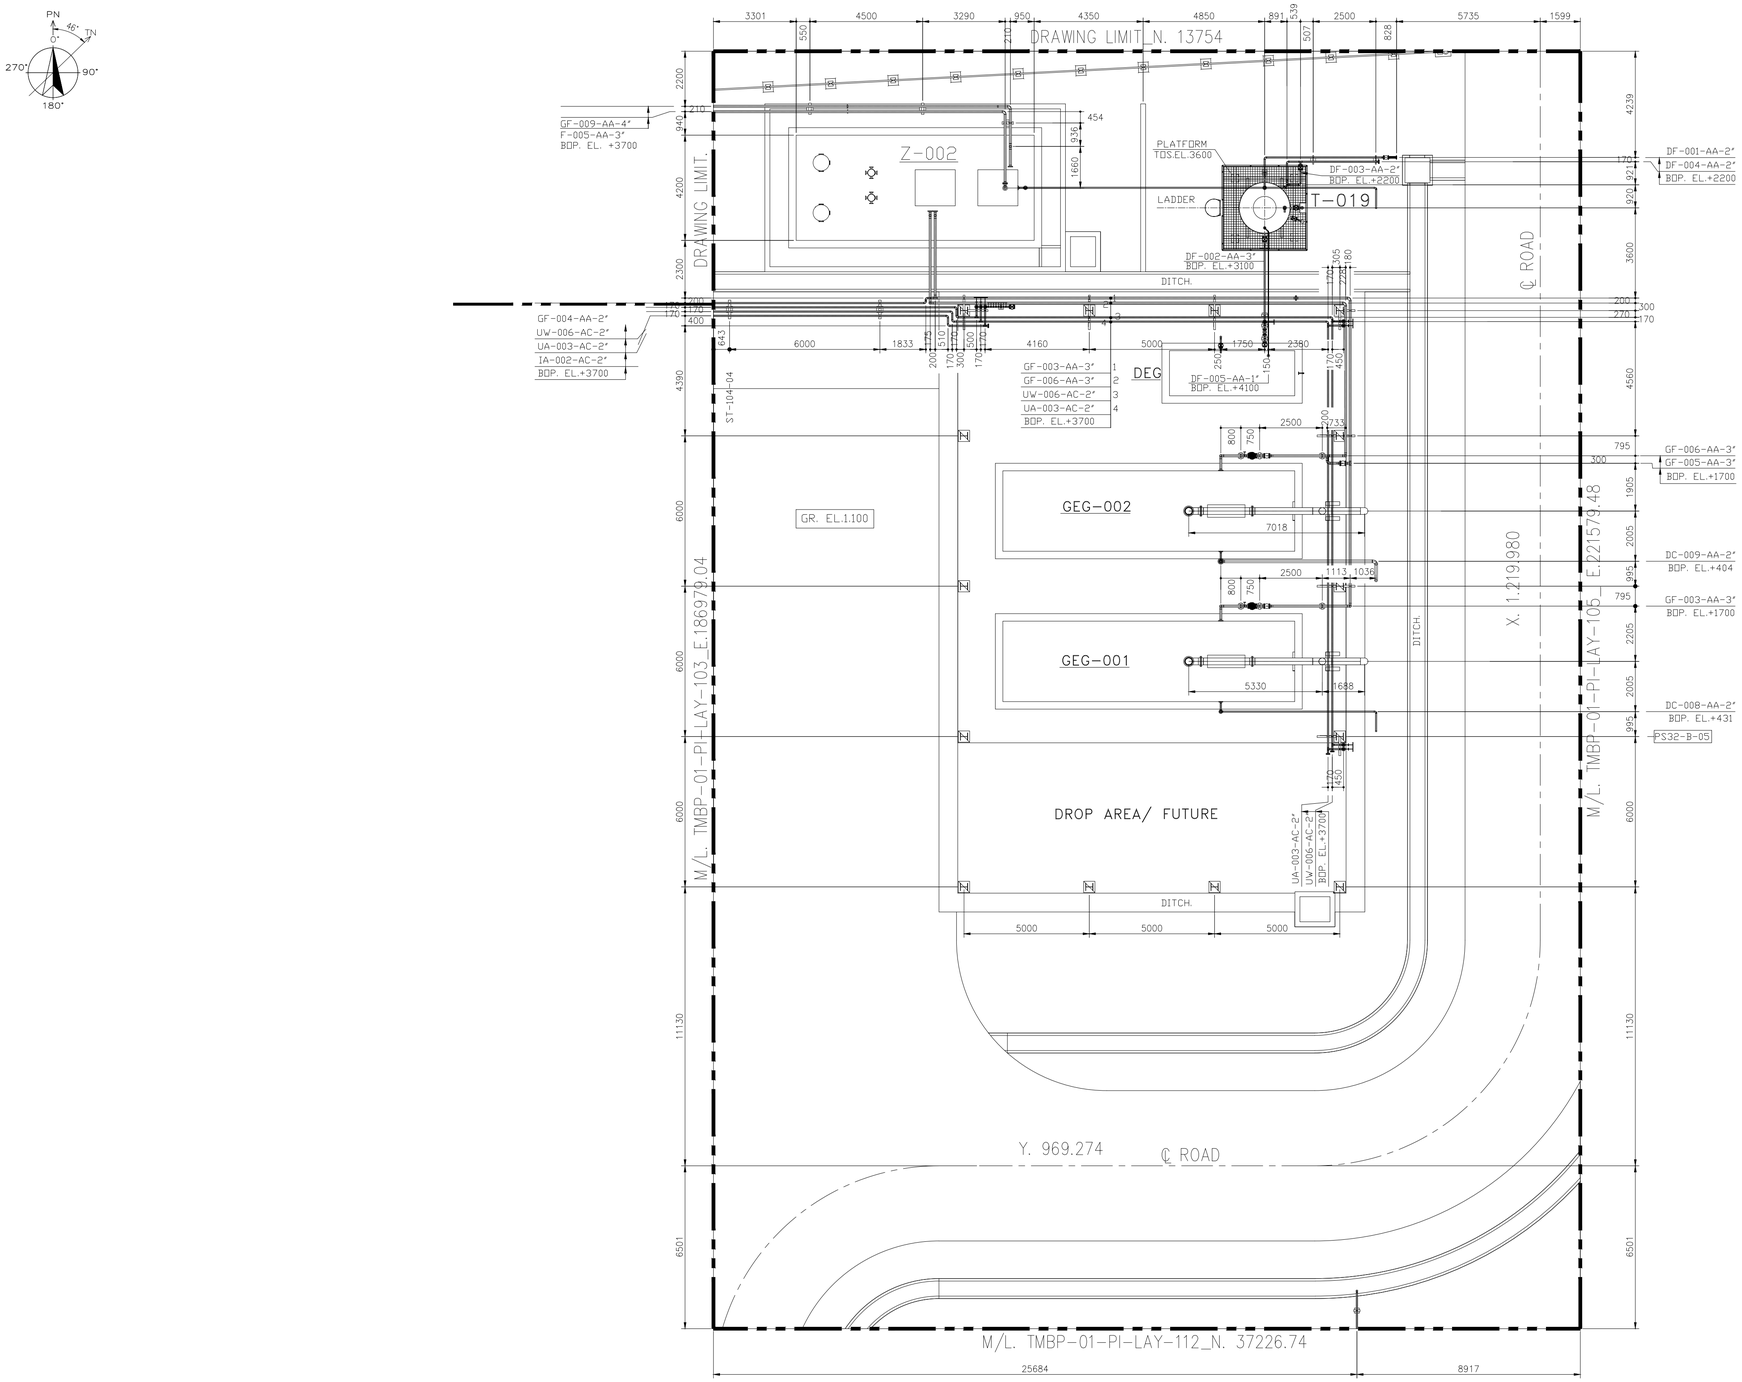

PLAN

KEY PLAN

THIS LOCATION

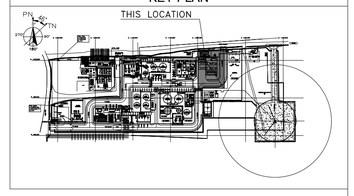

NOTE
1. ALL DIMENSIONS ARE IN MILLIMETERS, ELEVATION AND COORDINATE ARE IN METERS UNLESS OTHERWISE NOTED.
2. FINISH GROUND LEVEL EL = 0,00 = MSL+34.000

REFERENSI GAMBAR	DESKRIPSI REFERENSI	REV.	TANGGAL	URAIAN PERUBAHAN GAMBAR	DIGAMBAR	DIPERIKSA	DIPERIKSA	DISETUJUI
TMBP-SP001-PI-PLP-D101	OVERALL PLOT PLAN							
TMBP-SP001-PI-PLP-D102	PLOT PLAN							
TMBP-SP001-PI-DNX-D101	DRAWING INDEX/KEY PLAN	A	24/12/2025	ISSUED FOR REVIEW	AGS	–		

PT. PERTAMINA HULU ROKAN APPROVAL

PROYEK: JASA PEMBANGUNAN FASILITAS PRODUKSI STASIUN PENGUMPUL (SP) TANJUNG MIRING BARAT & KARANGAN TIMUR

PEMILIK PROYEK: skkmigas PERTAMINA EP

KONTRAKTOR: POG

SKALA:	NOMOR GAMBAR:	SHEET. NO.	REV
1:100	TMBP-SP001-PI-LAY-D104	1 OF 1	A

JUDUL GAMBAR:

PIPING LAYOUT AROUND DIESEL FUEL GAS SYSTEM, DEG, GEG