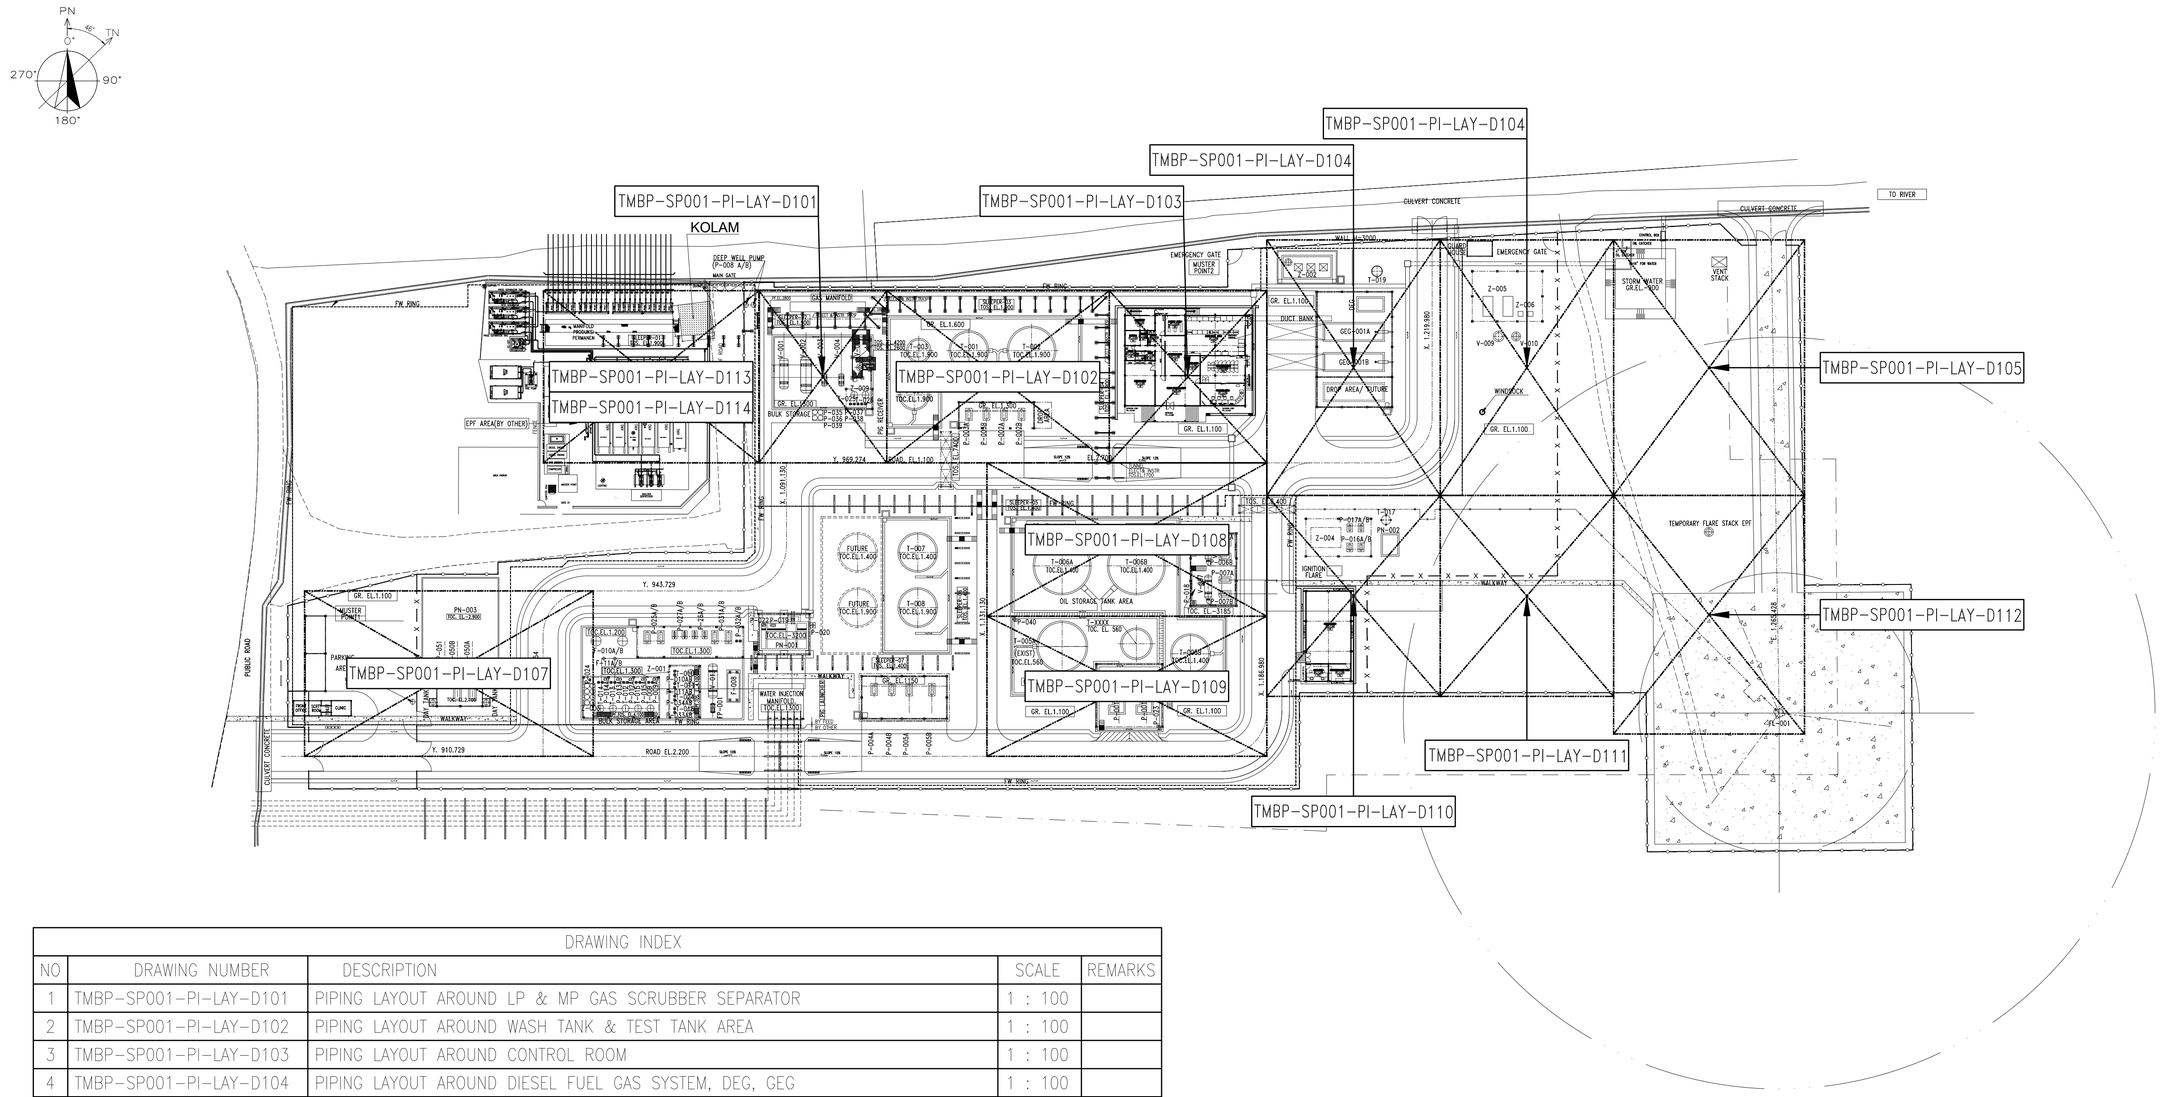

DRAWING INDEX				
NO	DRAWING NUMBER	DESCRIPTION	SCALE	REMARKS
1	TMBP-SP001-PI-LAY-D101	PIPING LAYOUT AROUND LP & MP GAS SCRUBBER SEPARATOR	1 : 100	
2	TMBP-SP001-PI-LAY-D102	PIPING LAYOUT AROUND WASH TANK & TEST TANK AREA	1 : 100	
3	TMBP-SP001-PI-LAY-D103	PIPING LAYOUT AROUND CONTROL ROOM	1 : 100	
4	TMBP-SP001-PI-LAY-D104	PIPING LAYOUT AROUND DIESEL FUEL GAS SYSTEM, DEG, GEG	1 : 100	
5	TMBP-SP001-PI-LAY-D105	PIPING LAYOUT AROUND INSTRUMENT AIR SYSTEM	1 : 100	
6	TMBP-SP001-PI-LAY-D106	PIPING LAYOUT AROUND VENT STACK AREA	1 : 100	
7	TMBP-SP001-PI-LAY-D107	PIPING LAYOUT AROUND FIRE WATER POUND AREA	1 : 100	
8	TMBP-SP001-PI-LAY-D108	PIPING LAYOUT AROUND STORAGE TANK KRG, KO DRUM & CLOSED DRAIN AREA	1 : 100	
9	TMBP-SP001-PI-LAY-D109	PIPING LAYOUT AROUND STORAGE TANK TMB & TRANSFER PUMP AREA	1 : 100	
10	TMBP-SP001-PI-LAY-D110	PIPING LAYOUT AROUND IGNITION FLARE AREA & SERVICE WATER AREA	1 : 100	
11	TMBP-SP001-PI-LAY-D111	PIPING LAYOUT AROUND FLARE (STANCHION) AREA	1 : 100	
12	TMBP-SP001-PI-LAY-D112	PIPING LAYOUT AROUND FLARE AREA	1 : 100	
13	TMBP-SP001-PI-LAY-D113	PIPING LAYOUT AROUND PRODUCTION MANIFOLD PERMANENT	1 : 100	
14	TMBP-SP001-PI-LAY-D114	PIPING SECTION DRAWING AROUND PRODUCTION MANIFOLD PERMANENT	1 : 100	

NOTE
1. ALL DIMENSIONS ARE IN MILLIMETERS, ELEVATION AND COORDINATE ARE IN METERS UNLESS OTHERWISE NOTED.
2. FINISH GROUND LEVEL EL = 0,00 = MSL+34.000

REFERENSI GAMBAR	DESKRIPSI REFERENSI	REV.	TANGGAL	URAIAN PERUBAHAN GAMBAR	DIGAMBAR	DIPERIKSA	DIPERIKSA	DISETUJUI
TMBP-SP001-PI-PLP-D101	OVERALL PLOT PLAN DRWG	A	22/12/2025	ISSUED FOR REVIEW	AG	–		

PT. PERTAMINA HULU ROKAN APPROVAL

PROYEK: JASA PEMBANGUNAN FASILITAS PRODUKSI STASIUN PENGUMPUL (SP) TANJUNG MIRING BARAT & KARANGAN TIMUR

PEMILIK PROYEK: skkmigas PERTAMINA EP

KONTRAKTOR: POG

SKALA:	NOMOR GAMBAR:	SHEET. NO.	REV
1:600	TMBP-SP001-PI-DNX-D101	1 OF 1	A

JUDUL GAMBAR: KEY PLAN / DRAWING INDEX