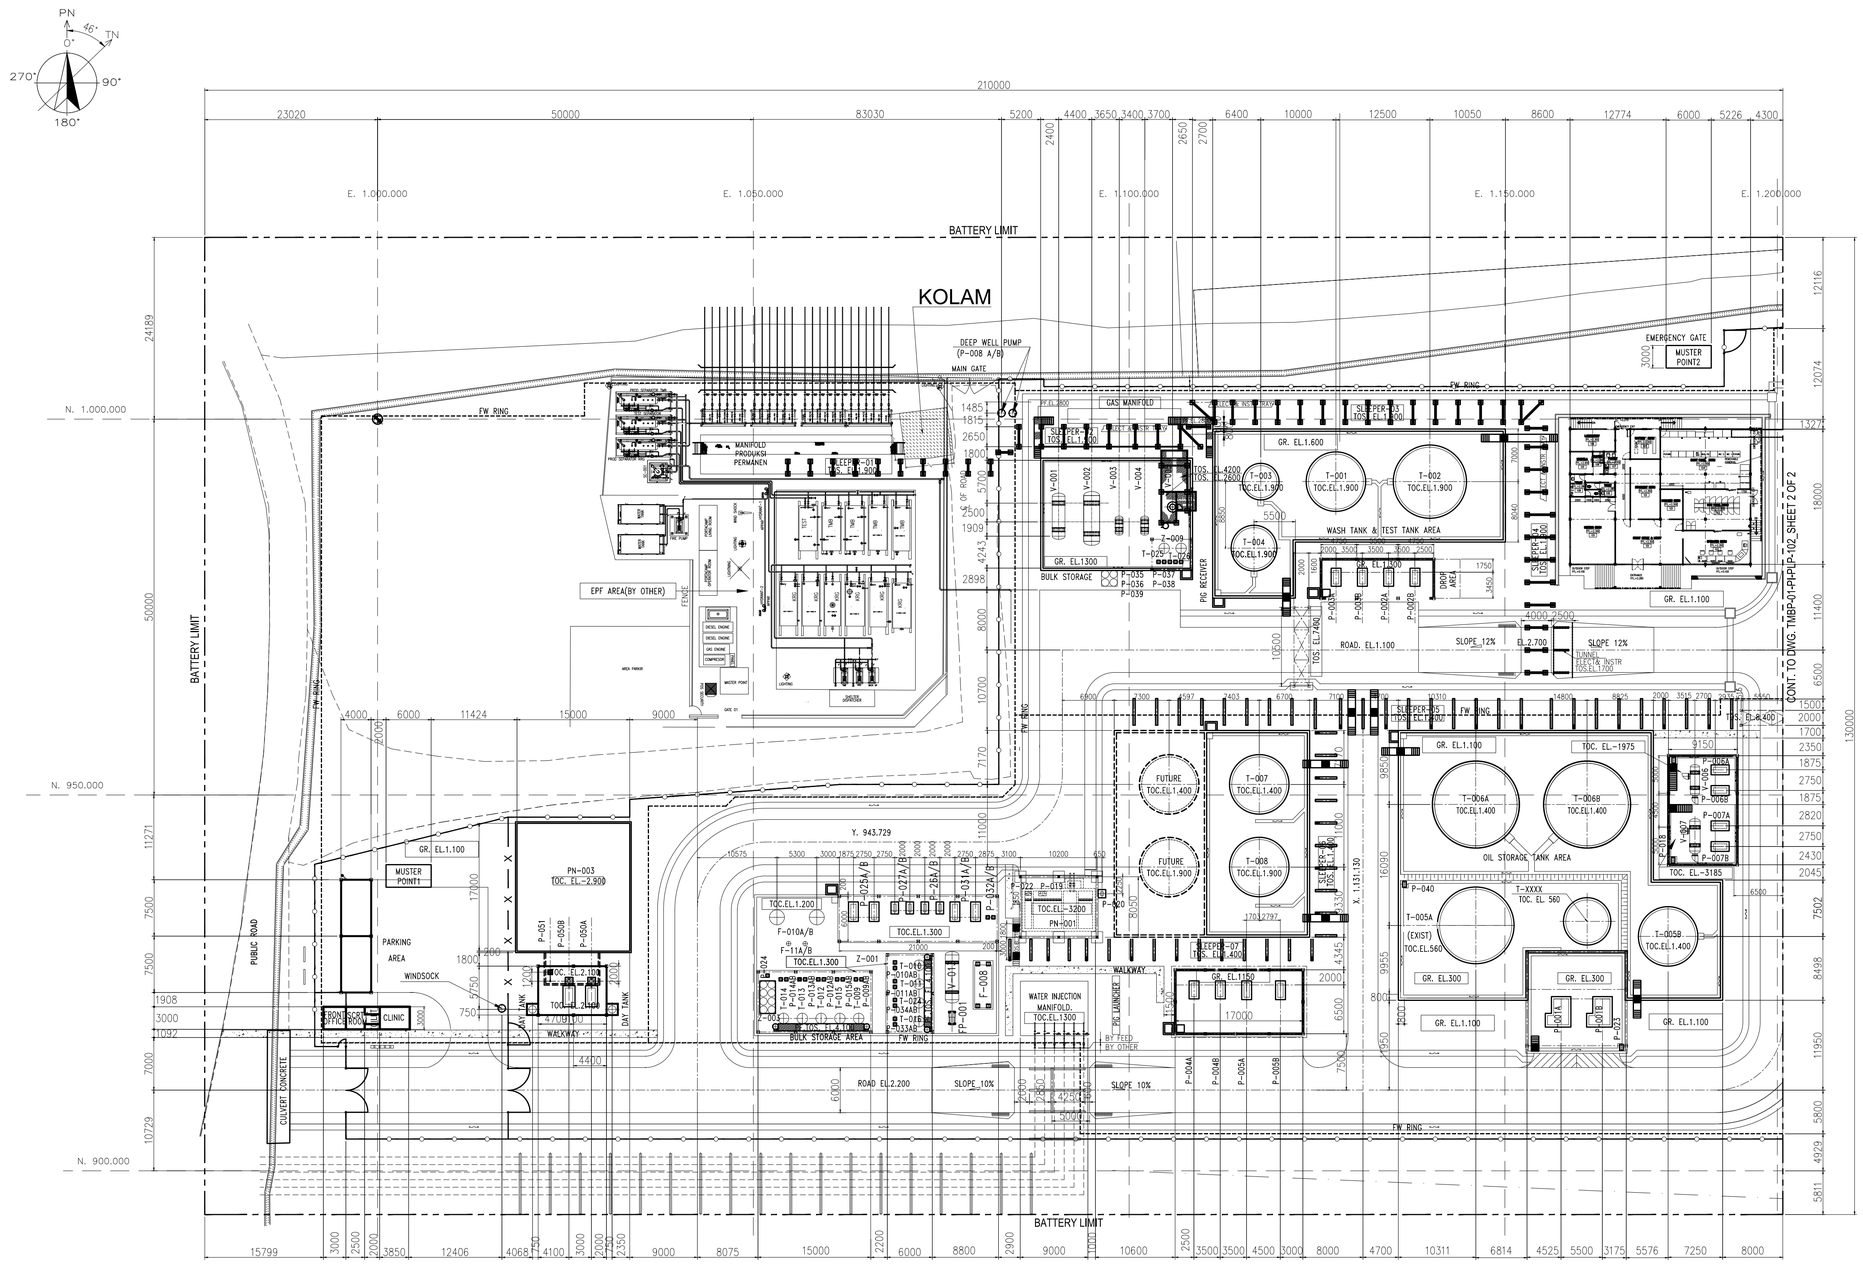

EQUIPMENT LIST			
NO	TAG. NO.	DESCRIPTION	GIRD
1	PN-003	FIRE WATER POND	B4
2	P-025A/B	VERTICAL FIRE WATER PUMP	C4
3	P-026	JOCKEY PUMP	C4
4	P-005A/B	WATER INJECTION PUMP	B7
5	P-004A/B	FEED WATER PUMP	B7
6	Z-001	WTP PACKAGE	C5
7	Z-003	CHEMICAL INJECTION PACKAGE	B5
8	PN-001	SUMP PIT	C6
9	P-002A/B	TEST PUMP TMB	D8
10	P-003A/B	TEST PUMP KRG	D8
11	P-001A/B	GROSS TRANSFER PUMP	B9
12	V-001	PROD. SEPARATOR TMB	E6
13	V-002	PROD. SEPARATOR KRG	E6
14	V-003	TEST SEPARATOR TMB	E6
15	V-004	TEST SEPARATOR KRG	E6
16	V-005	PROD. SCRUBBER	E6
17	–	CONTROL ROOM	E9
24	V-006	KNOCK OUT DRUM VESSEL	C9
25	V-007	CLOSED DRAIN VESSEL	C9
28	T-001	WASH TANK TMB	E7
29	T-002	WASH TANK KRG	E8
30	T-003	TEST TANK TMB	E7
31	T-004	TEST TANK KRG	D7
32	T-007	PRODUCED WATER TANK	C7
33	T-008	TREATED WATER TANK	C7
34	T-005B	STORAGE TANK TMB	B9
35	T-006A	STORAGE TANK KRG	C8
36	T-006B	STORAGE TANK KRG	C9
37	T-005A (EXISTING)	STORAGE TANK TMB (EXISTING)	C8
38	P-006A/B	KOD PUMP	C9
39	P-007A/B	CLOSED DRAIN PUMP	C9
40	P-018	CLOSE DRAIN SUMP PUMP	C9
41	P-019	WATER SUMP PUMP	C6
44	P-020	SLURRY PUMP	C6
45	P-021	KOD SUMP PUMP	D6
46	P-022	OIL SUMP PUMP	C9
51	P-008A/B	DEEP WELL PUMP	E6
52	P-023	GROSS SUMP PUMP	B8

NOTE

1. ALL DIMENSIONS ARE IN MILLIMETERS, ELEVATION AND COORDINATE ARE IN METERS UNLESS OTHERWISE NOTED.
2. FINISH GROUND LEVEL EL = 0,00 = MSL+34.000

REFERENSI GAMBAR	DESKRIPSI REFERENSI	REV.	TANGGAL	URAIAN PERUBAHAN GAMBAR	DIGAMBAR	DIPERIKSA	DIPERIKSA	DISETUJUI
TMBP-SP001-PI-PLP-D101	OVERALL PLOT PLAN DRWG	A	30/12/2025	ISSUED FOR REVIEW	AG	–		

PT. PERTAMINA HULU ROKAN APPROVAL

PROYEK: JASA PEMBANGUNAN FASILITAS PRODUKSI STASIUN PENGUMPUL (SP) TANJUNG MIRING BARAT & KARANGAN TIMUR

PEMILIK PROYEK: skkmigas PERTAMINA EP

KONTRAKTOR: POG

SKALA: 1:400

NOMOR GAMBAR: TMBP-SP001-PI-PLP-D102

SHEET. NO.: 1 OF 2

REV: A

JUDUL GAMBAR: PLOT PLAN DRAWING

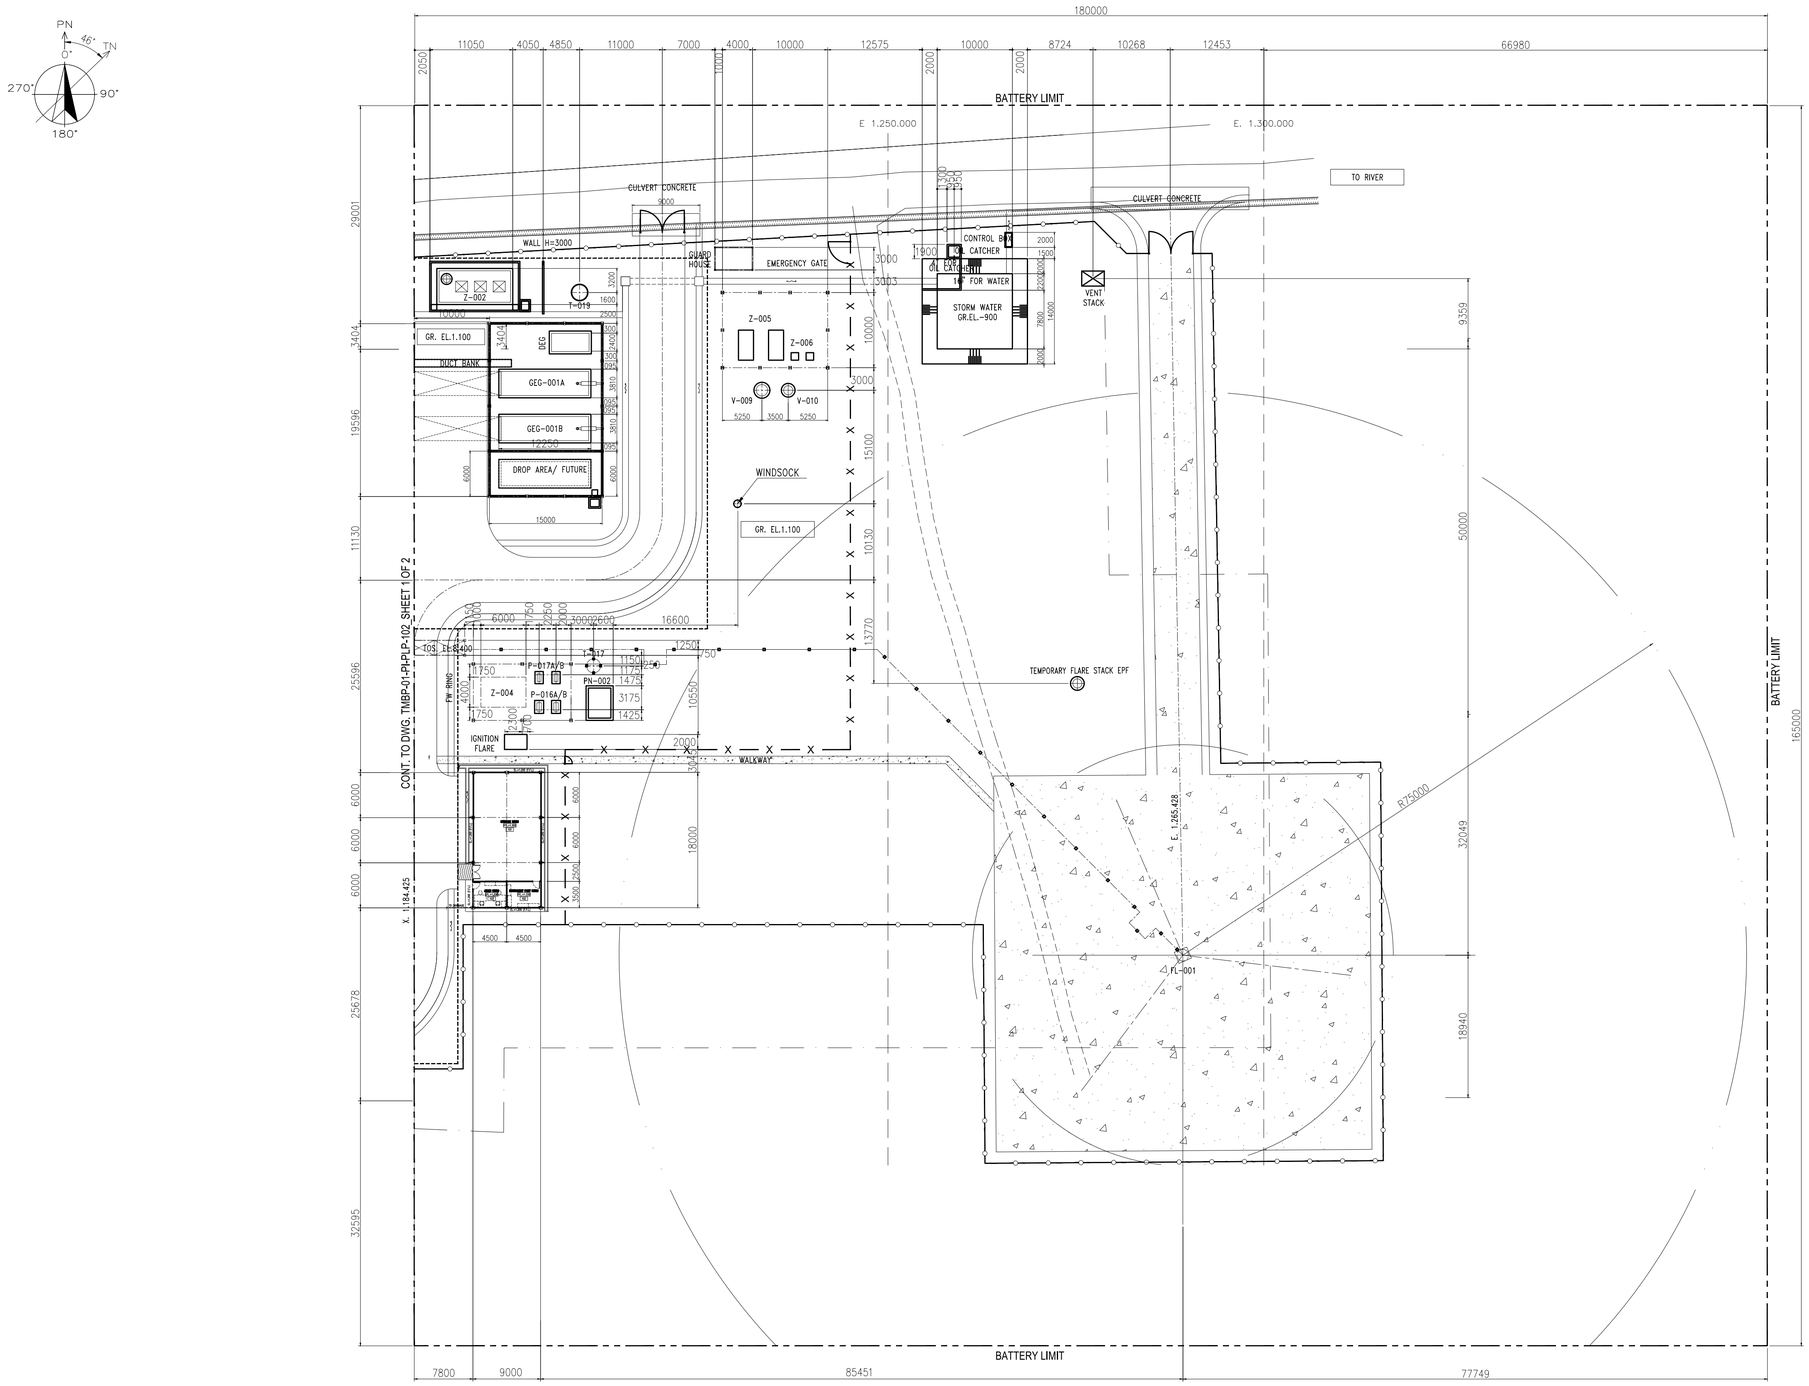

EQUIPMENT LIST			
NO	TAG. NO.	DESCRIPTION	GIRD
18	–	WAREHOUSE & WORKSHOP	D2
19	Z-002	FUEL GAS PACKAGE	C2
20	GEG-001	GAS ENGINE GENERATOR	F2
21	GEG-002	GAS ENGINE GENERATOR	F2
22	DEG-001	DIESEL ENGINE GENERATOR	F2
23	Z-005,V-009,V-010	IA/PA PACKAGE	F3
26	FL-001	FLARE STACK	D5
27	P-016AB,P-017AB,PN-002	SERVICE WATER	E2
42	P-016A/B	BOSTER PUMP	E2
43	P-017A/B	WATER DISTRIBUTION PUMP	E2
47	T-019	DIESEL STORAGE TANK	G2
48	T-017	PORTABLE WATER TANK	E2
49	Z-004	WATER TREATMENT PACKAGE	E2
50	PN-002	WATER POND	E2

NOTE

1. ALL DIMENSIONS ARE IN MILLIMETERS, ELEVATION AND COORDINATE ARE IN METERS UNLESS OTHERWISE NOTED.
2. FINISH GROUND LEVEL EL = 0,00 = MSL+34.000

REFERENSI GAMBAR	DESKRIPSI REFERENSI	REV.	TANGGAL	URAIAN PERUBAHAN GAMBAR	DIGAMBAR	DIPERIKSA	DIPERIKSA	DISETUJUI
TMBP-SP001-PI-PLP-D101	OVERALL PLOT PLAN DRWG	A	30/12/2025	ISSUED FOR REVIEW	AG	–		

PT. PERTAMINA HULU ROKAN APPROVAL

PROYEK:
JASA PEMBANGUNAN FASILITAS PRODUKSI STASIUN PENGUMPUL (SP) TANJUNG MIRING BARAT & KARANGAN TIMUR

PEMILIK PROYEK:
skkmigas PERTAMINA EP

KONTRAKTOR:
POG

SKALA: 1:400

NOMOR GAMBAR: TMBP-SP001-PI-PLP-D102

SHEET. NO. 2 OF 2

REV A

JUDUL GAMBAR:
PLOT PLAN DRAWING