NO	PARTS	SPESIFICATION OF MATERIAL	SIZE	QTY.
1	TUBE	SEAMLESS ANNEALED STAINLESS TUBE, A-269-T-316,SS316L	1/2"OD X 0.035"WT	3M
2	MALE CONNECTOR	DOUBLE FERRULE, COMPRESSION TYPE, SS316	1/2"OD X 1/2"NPTM	1EA
3	MALE CONNECTOR	DOUBLE FERRULE, COMPRESSION TYPE, SS316	1/2"OD X 1/4"NPTM	1EA

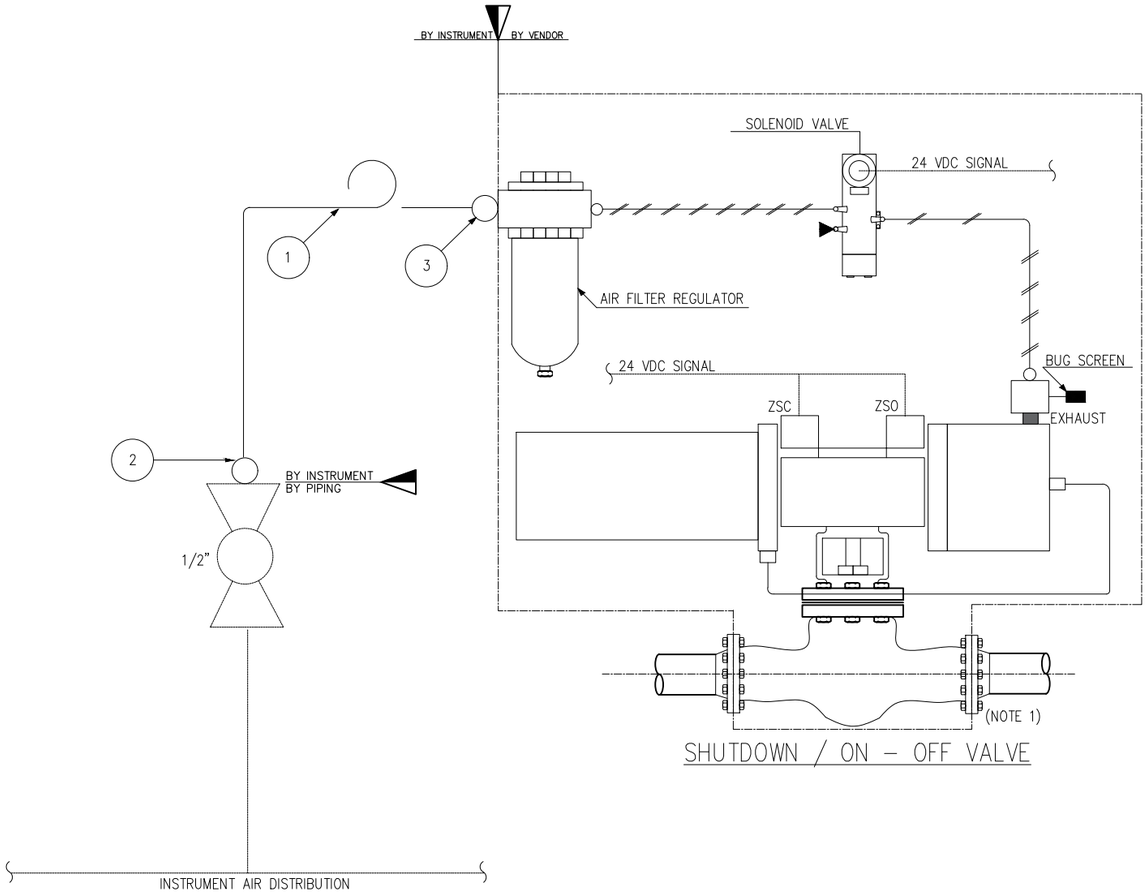

LIST FIELD INSTRUMENT

NO.	TAG. NO.	SERVICE	PROCESS PIPING / EQUIPMENT CLASS	PROCESS PIPING / EQUIPMENT SIZE	STREAM TRACE	P & ID NO.
1	SDV-V001-001	PRODUCTION SEPARATOR TMB	150#	6"	-	TMBP-01-PR-PID-101
2	SDV-V001-002	PRODUCTION SEPARATOR TMB	150#	3"	-	TMBP-01-PR-PID-101
3	SDV-V003-001	TEST SEPARATOR TMB	150#	3"	-	TMBP-01-PR-PID-101
4	SDV-V003-002	TEST SEPARATOR TMB	150#	2"	-	TMBP-01-PR-PID-101
5	SDV-V002-001	PRODUCTION SEPARATOR KRG	150#	6"	-	TMBP-01-PR-PID-102
6	SDV-V002-002	PRODUCTION SEPARATOR KRG	150#	4"	-	TMBP-01-PR-PID-102
7	SDV-V004-001	TES SEPARATOR KRG	150#	6"	-	TMBP-01-PR-PID-102
8	SDV-V004-002	TES SEPARATOR KRG	150#	2"	-	TMBP-01-PR-PID-102
9	SDV-P005-001	INJECTION PUMP	150#	3"	-	TMBP-01-PR-PID-113
10	BDV-V005-001	PRODUCTION SCRUBBER	150#	6"	-	TMBP-01-PR-PID-114
11	SDV-V005-001	PRODUCTION SCRUBBER	150#	2"	-	TMBP-01-PR-PID-114
12	SDV-V005-002	PRODUCTION SCRUBBER	150#	6"	-	TMBP-01-PR-PID-114

NOTES :

1. GASKET, STUD BOLT & NUT SUPPLIED BY PIPING

DRAWING REFERENCE	DESCRIPTION	REV	DATE	DESCRIPTION	PREPR'D	CHECK'D	APRV'D	CHECKED	APPROVED
		A	31/12/2025	ISSUED FOR REVIEW	MHP	AS	RTN		

PT. PERTAMINA EP APPROVAL

PROJECT : JASA PEMBANGUNAN FASILITAS PRODUKSI STASIUN PENGUMPUL (SP) TANJUNG MIRING BARAT & KARANGAN TIMUR

OWNER : skkmigas PERTAMINA EP

CONTRACTOR : POG

SCALE : NTS

DRAWING NO. TMBP – SP001 – IN – HUP – D119

SHEET. NO. 1 OF 1

REV A

DRAWING TITLE : INSTRUMENT HOOK UP DIAGRAM AUTOMATIC VALVE SHUTDOWN & ON–OFF VALVE