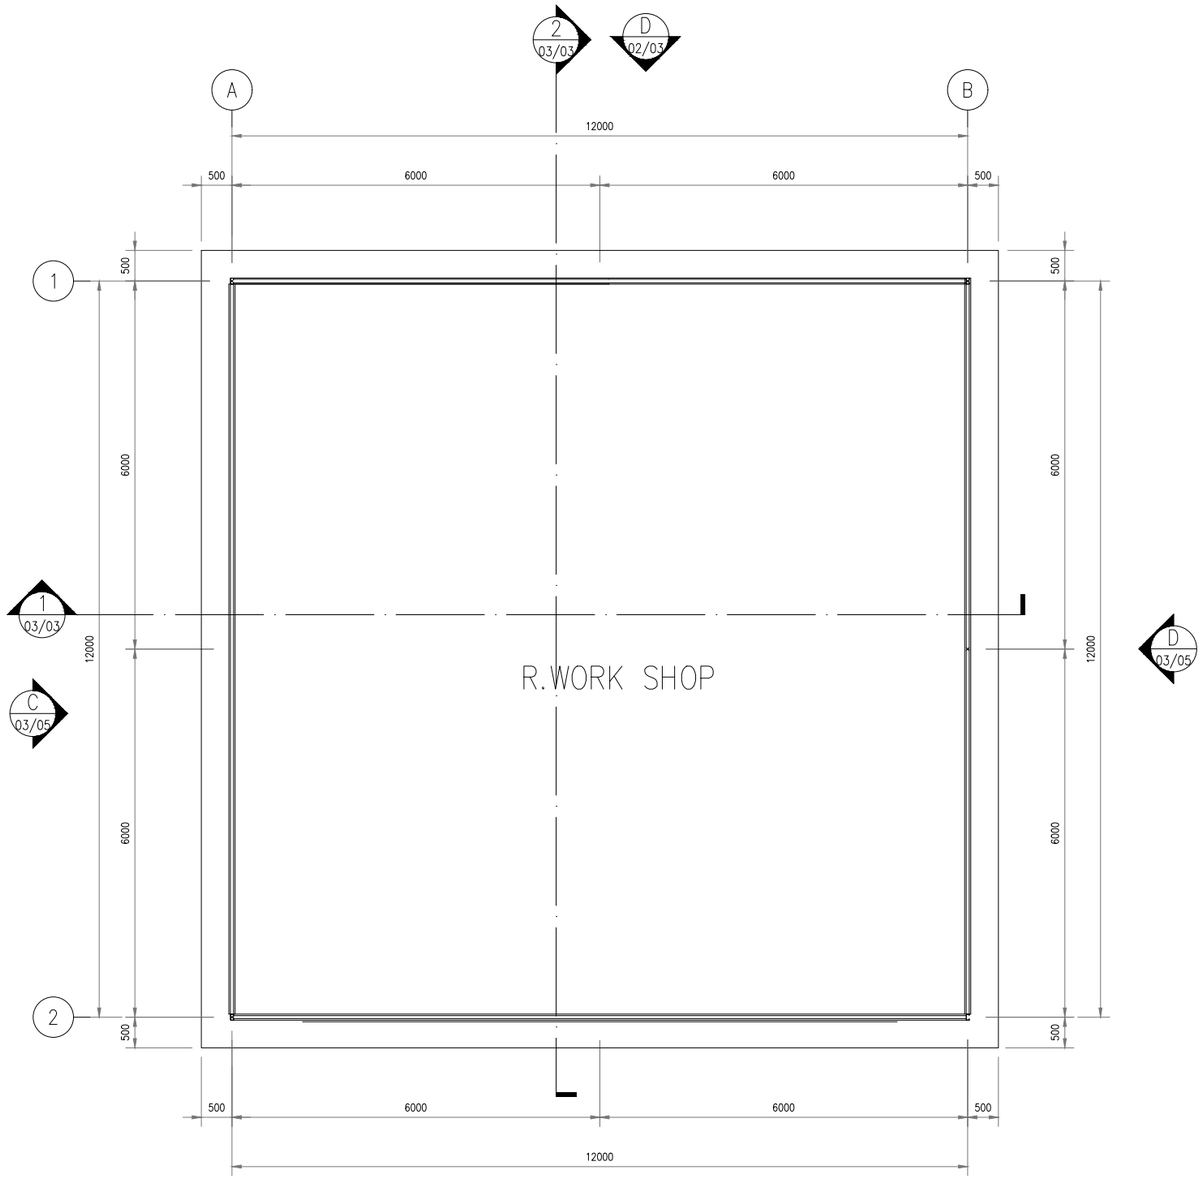

PLAN WORKSHOP

SKALA: 1:100

NOTES :

DRAWING REFERENCE	DESCRIPTION	REV	DATE	DESCRIPTION	PREPR'D	CHECK'D	APRV'D	CHECKED	APPROVED
		A	30-12-2025	ISSUED FOR REVIEW	NSR	AS	RTN		

PT. PERTAMINA EP APPROVAL

PROCET :

JASA PEMBANGUNAN FASILITAS PRODUKSI STASIUN PENGUMPUL (SP)
TANJUNG MIRING BARAT & KARANGAN TIMUR

OWNER : skkmigas PERTAMINA EP

CONTRACTOR : POG

SCALE : NTS

DRAWING NO. TMBP – SP001 – CS – DET – D109

SHEET. NO. 01 OF 06

REV A

DRAWING TITLE :

DRAWING FOR WORKSHOP

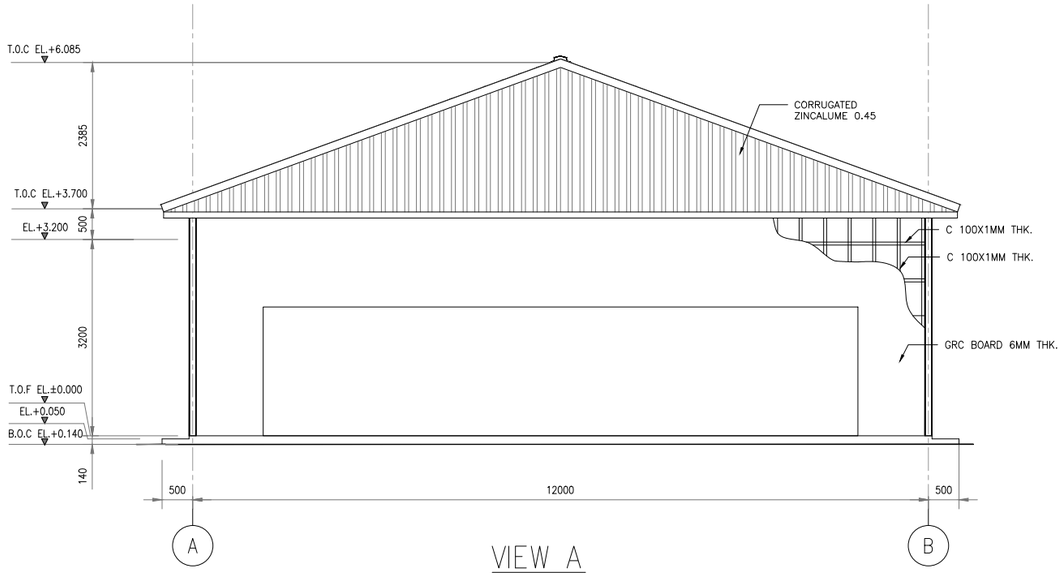

VIEW A
SKALA: 1:100

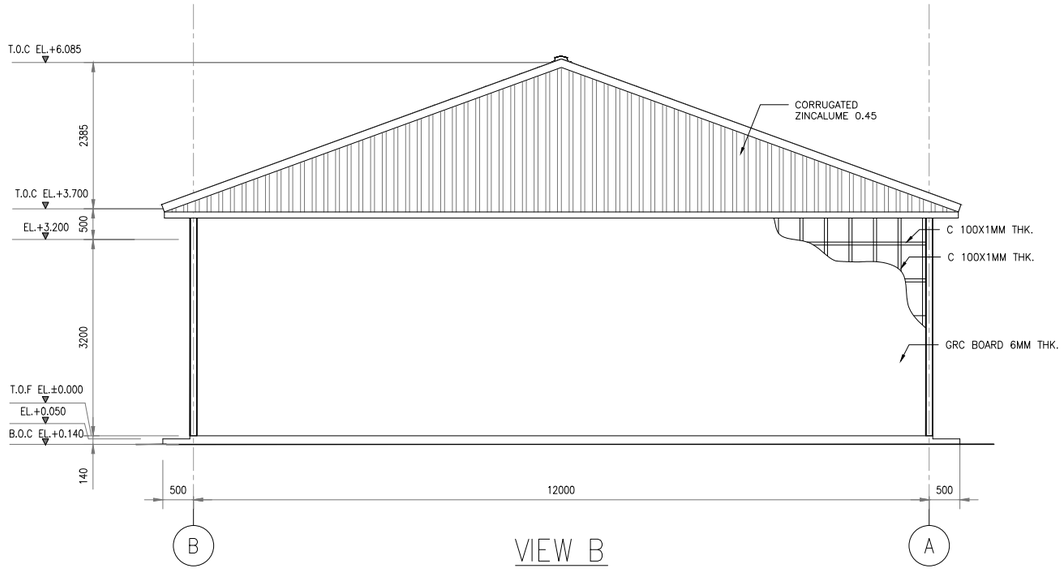

VIEW B
SKALA: 1:100

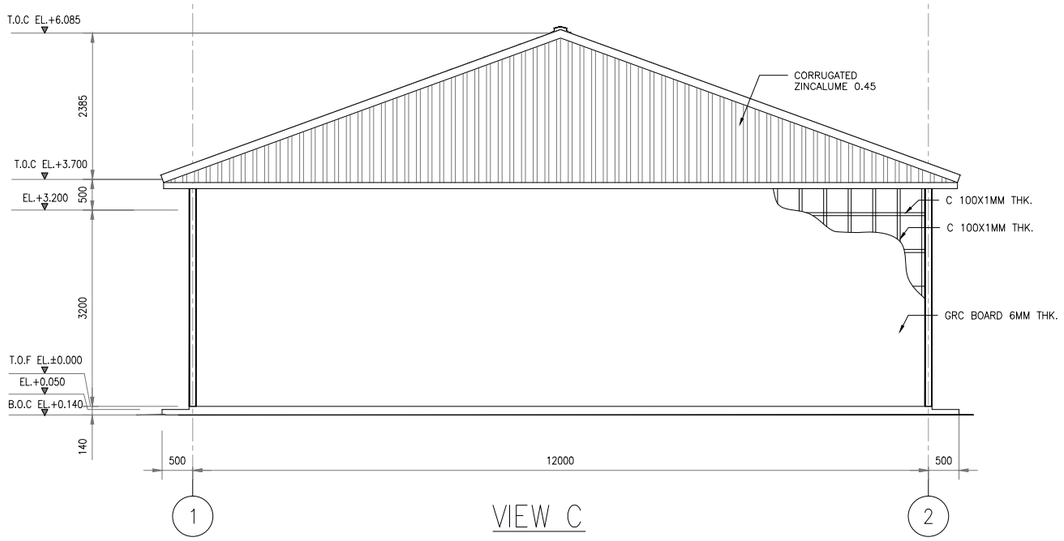

VIEW C
SKALA: 1:100

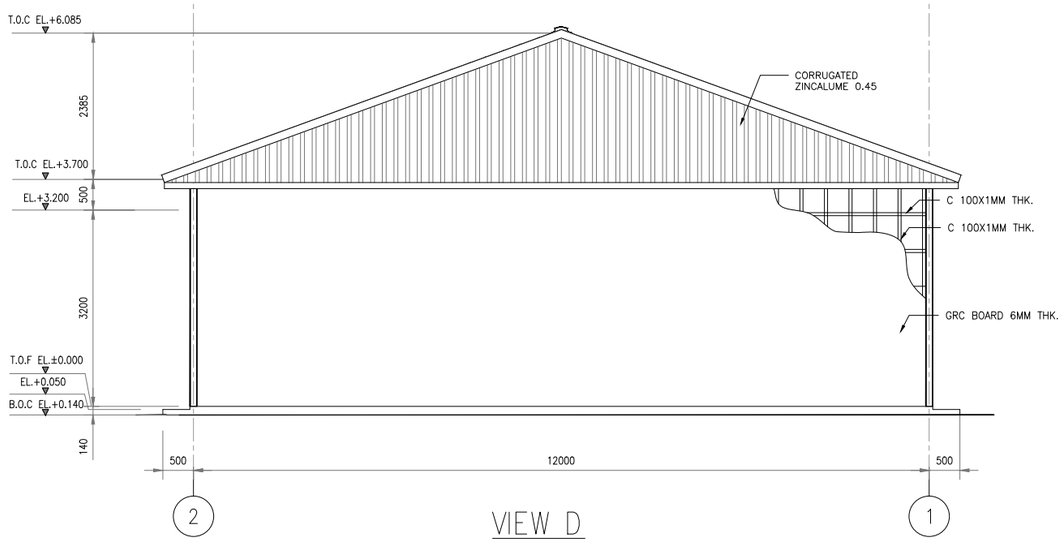

VIEW D
SKALA: 1:100

NOTES :

DRAWING REFERENCE	DESCRIPTION	REV	DATE	DESCRIPTION	PREPR'D	CHECK'D	APRV'D	CHECKED	APPROVED
		A	30-12-2025	ISSUED FOR REVIEW	NSR	AS	RTN		

PT. PERTAMINA EP APPROVAL

PROCET :
JASA PEMBANGUNAN FASILITAS PRODUKSI STASIUN PENGUMPUL (SP)
TANJUNG MIRING BARAT & KARANGAN TIMUR

OWNER : skkmigas PERTAMINA EP

CONTRACTOR : POG

SCALE : NTS

DRAWING NO. TMBP – SP001 – CS – DET – D109

SHEET. NO. 02 OF 06

REV A

DRAWING TITLE :
DRAWING FOR WORKSHOP

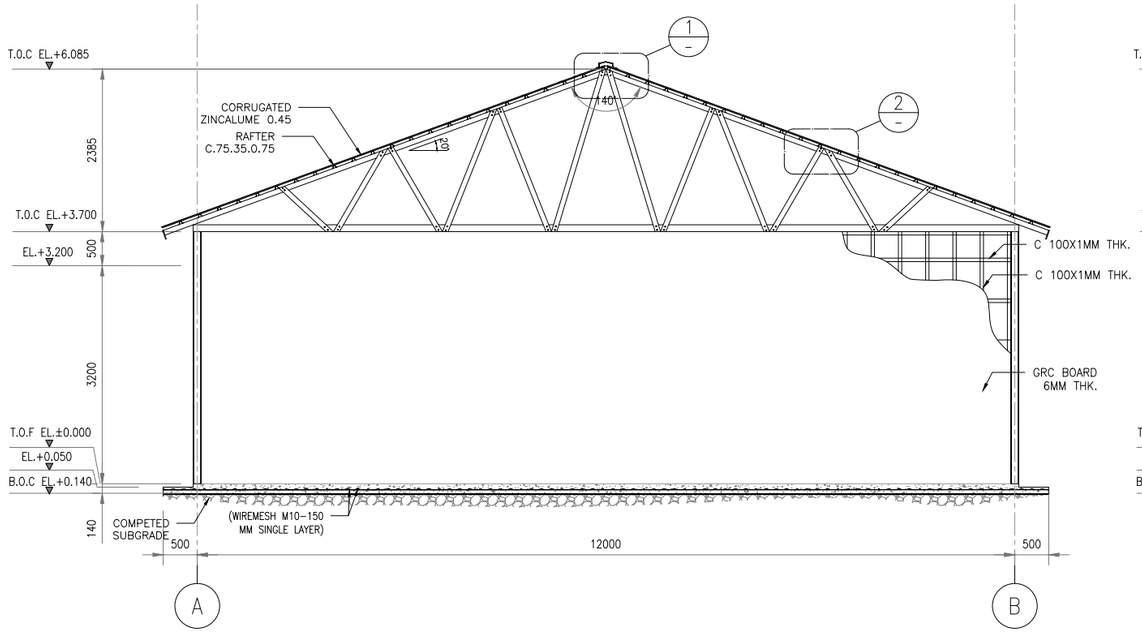

SECTION 1
SKALA: 1:100

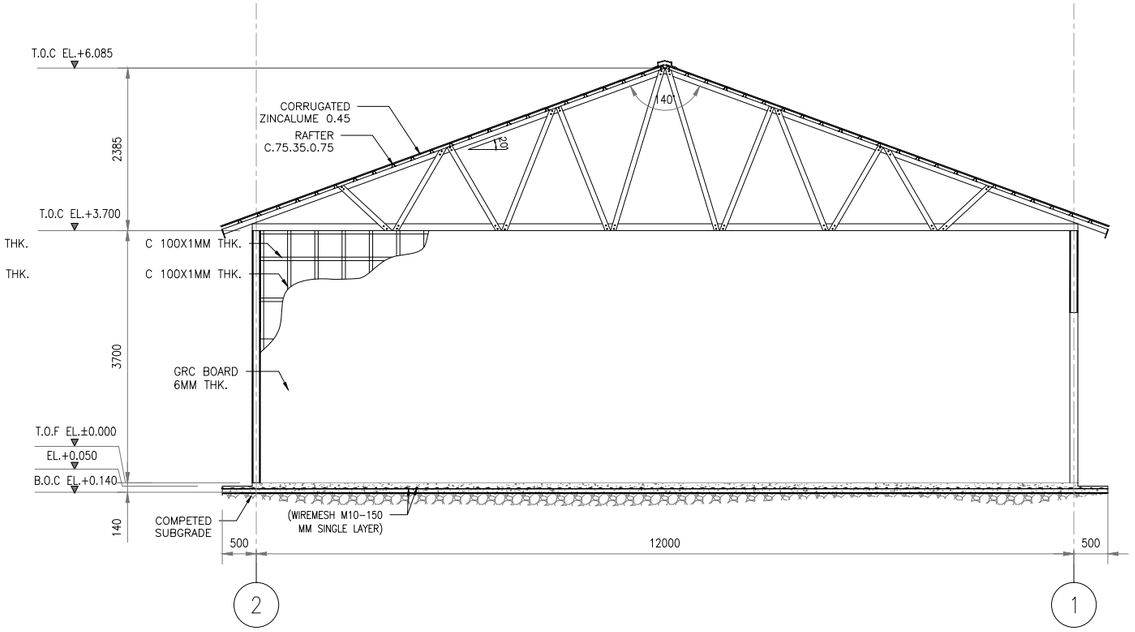

SECTION 2
SKALA: 1:100

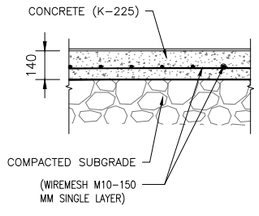

DETAIL FLOOR SLAB
SKALA: 1:30

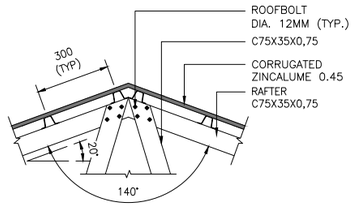

DETAIL 1
SKALA: 1:25

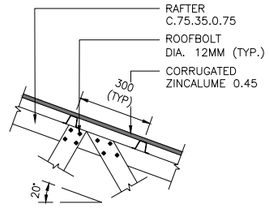

DETAIL 2
SKALA: 1:25

EXTERIOR FINISH SCHEDULE		
MARK	NAME	MATERIAL/SPECIFICATION
1	WALL	GRC BOARD 6MM THK.
2	ROOF	CORRUGATED ZINCALUME 0.45
3	COLUMN	C 100.50.20.3,2

NOTES :

DRAWING REFERENCE	DESCRIPTION	REV	DATE	DESCRIPTION	PREPR'D	CHECK'D	APRV'D	CHECKED	APPROVED
		A	30-12-2025	ISSUED FOR REVIEW	NSR	AS	RTN		

PT. PERTAMINA EP APPROVAL

PROCET :
JASA PEMBANGUNAN FASILITAS PRODUKSI STASIUN PENGUMPUL (SP) TANJUNG MIRING BARAT & KARANGAN TIMUR

OWNER : skkmigas PERTAMINA EP

CONTRACTOR : POG

SCALE : NTS

DRAWING NO. TMBP – SP001 – CS – DET – D109

SHEET. NO. 03 OF 06

REV A

DRAWING TITLE :
DRAWING FOR WORKSHOP