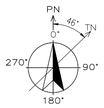

KEY PLAN

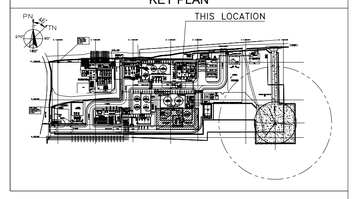

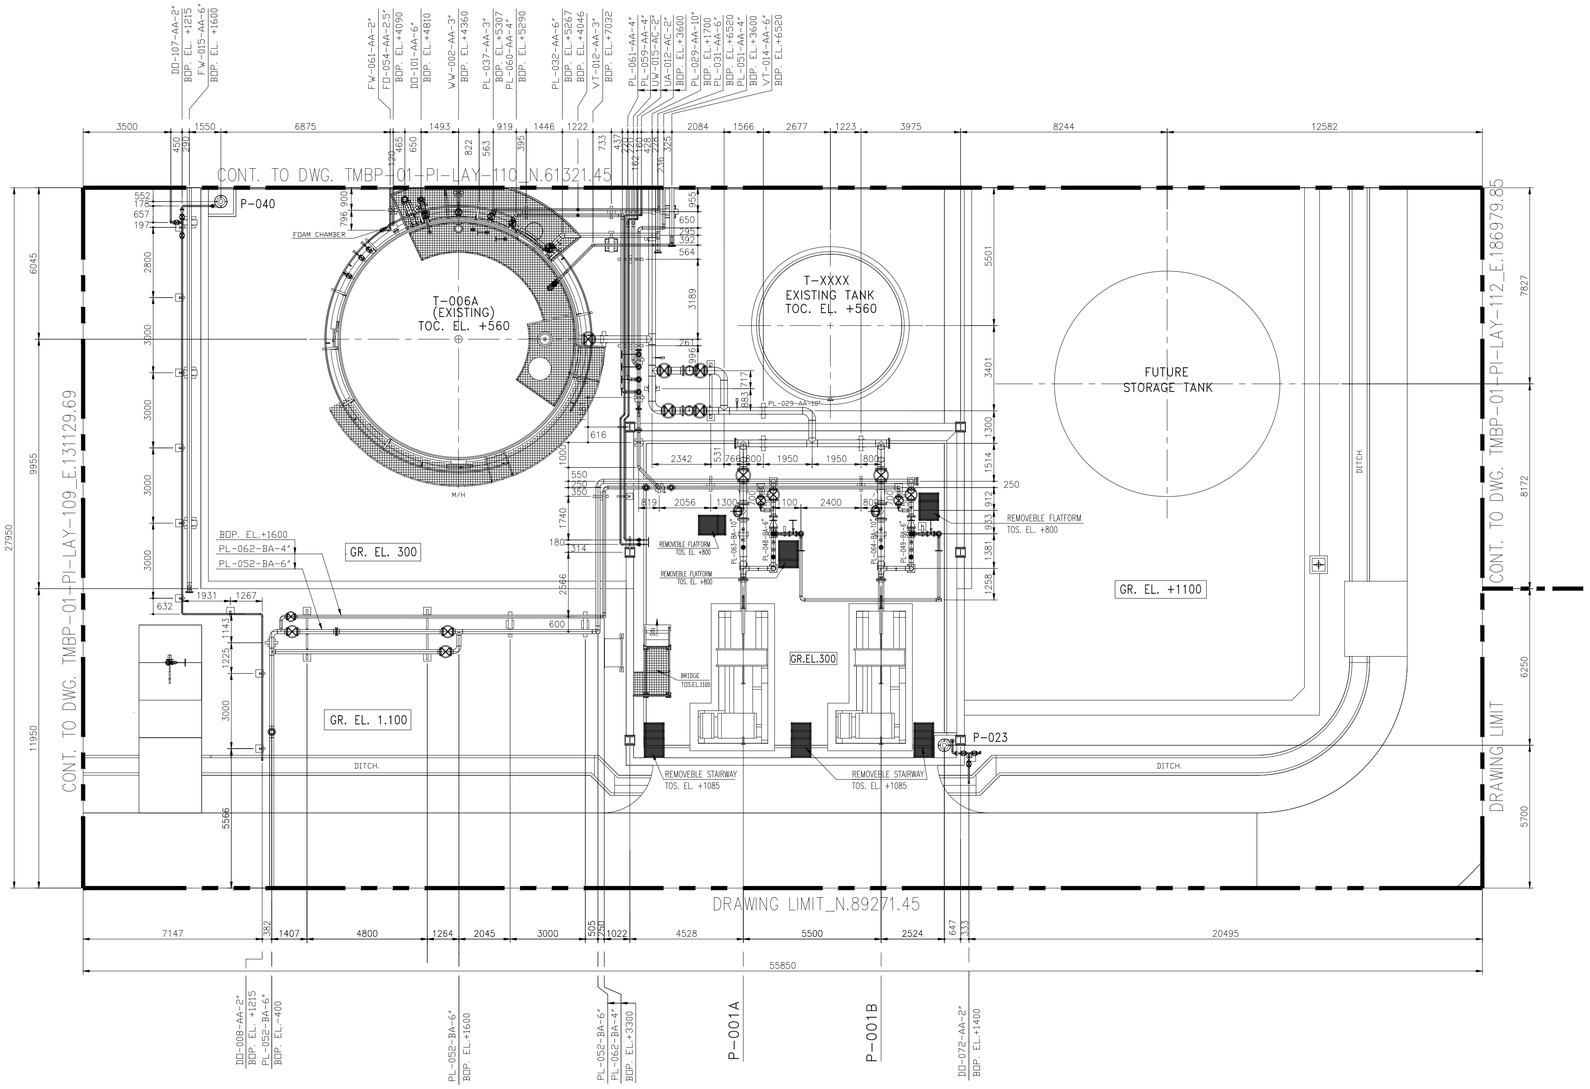

PLAN

NOTE
1. ALL DIMENSIONS ARE IN MILLIMETERS, ELEVATION AND COORDINATE ARE IN METERS UNLESS OTHERWISE NOTED.
2. FINISH GROUND LEVEL EL = 0,00 = MSL+34.000

DRAWING REFERENCE	DESCRIPTION	REV.	DATE	DESCRIPTION	BY	CHECKED
TMBP-SP001-PI-PLP-D101	OVERALL PLOT PLAN					
TMBP-SP001-PI-PLP-D102	PLOT PLAN					
TMBP-SP001-PI-DNX-D101	DRAWING INDEX/KEY PLAN	A	31/12/2025	ISSUED FOR REVIEW	AGS	–

PT. PERTAMINA HULU ROKAN APPROVAL

CHECKED	APPROVED

PROJECT :
JASA PEMBANGUNAN FASILITAS PRODUKSI STASIUN PENGUMPUL (SP) TANJUNG MIRING BARAT & KARANGAN TIMUR

OWNER :
skkmigas PERTAMINA EP

CONTRACTOR:
POG

SCALE :	DRAWING NO :	SHEET. NO.	REV
1:100	TMBP-SP001-PI-LAY-D109	1 OF 1	A

DRAWING TITLE :
PIPING LAYOUT AROUND STORAGE TANK TMB & TRANSFER PUMP AREA