


PLAN

KEY PLAN

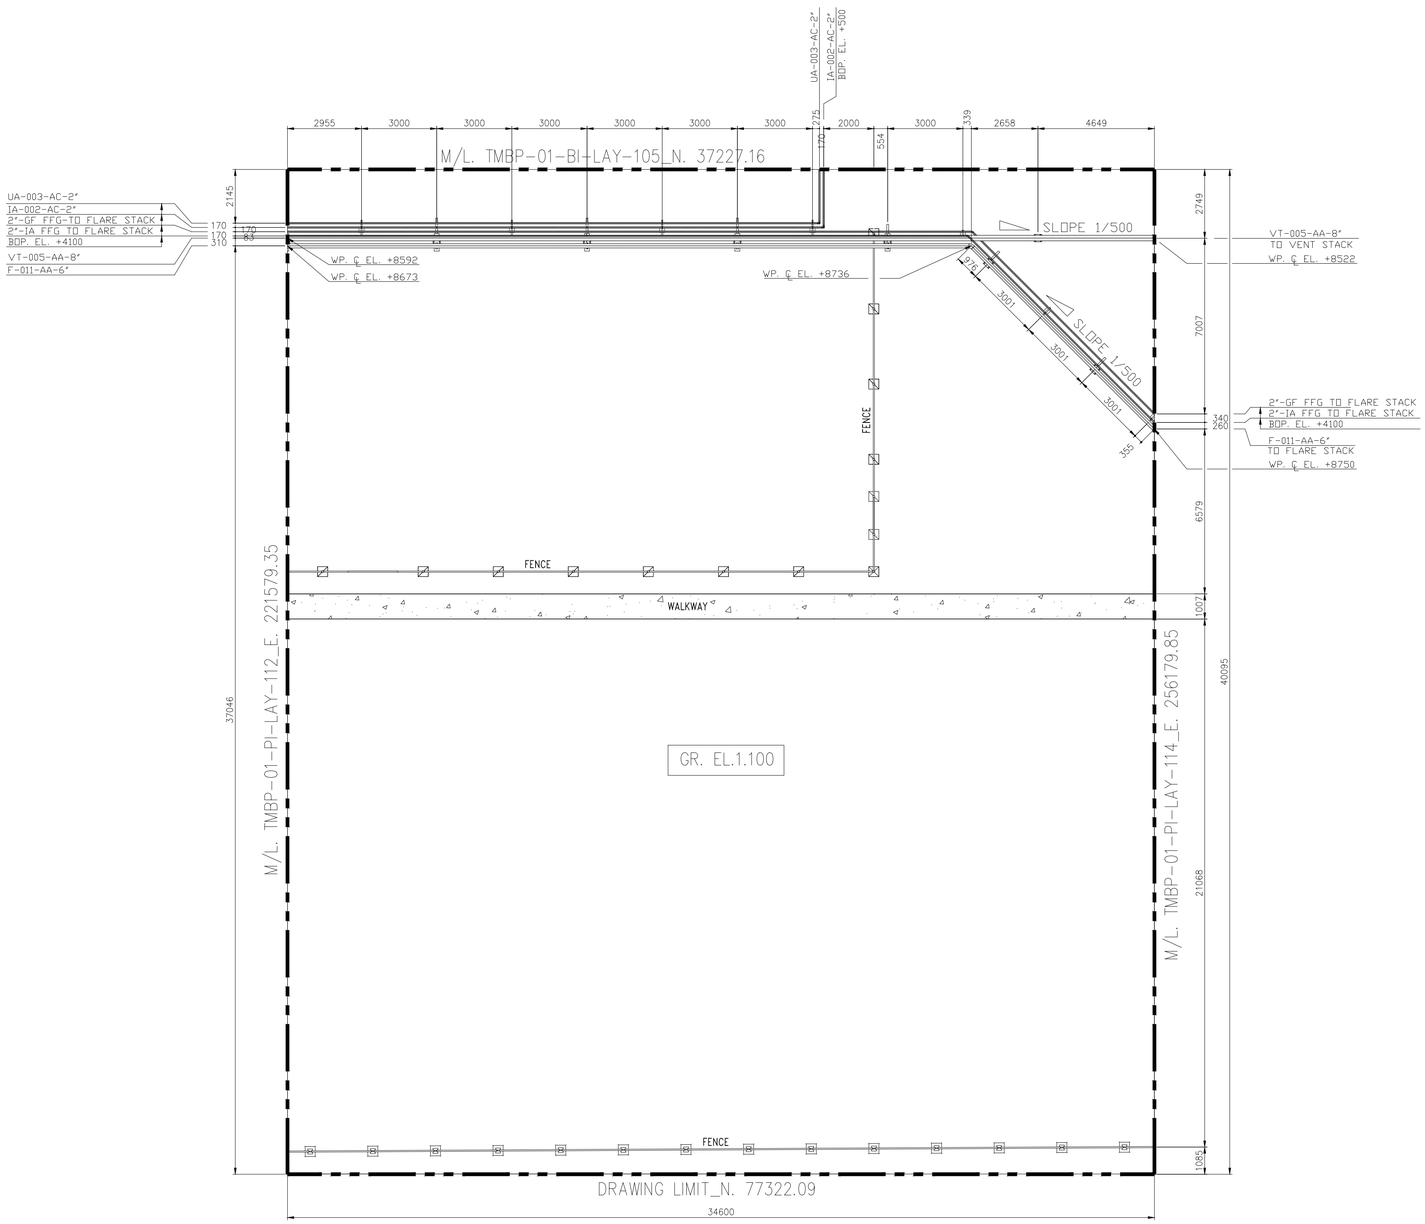


NOTE
1. ALL DIMENSIONS ARE IN MILLIMETERS, ELEVATION AND COORDINATE ARE IN METERS UNLESS OTHERWISE NOTED.
2. FINISH GROUND LEVEL EL = 0,00 = MSL+34.000

| DRAWING REFERENCE | DESCRIPTION | REV. | DATE | DESCRIPTION | BY | CHECKED |
|---|---|---|---|---|---|---|
| TMBP-SP001-PI-PLP-D101 | OVERALL PLOT PLAN | | | | | |
| TMBP-SP001-PI-PLP-D102 | PLOT PLAN | | | | | |
| TMBP-SP001-PI-DNX-D101 | DRAWING INDEX/KEY PLAN | A | 01/01/2026 | ISSUED FOR REVIEW | AGS | – |

PT. PERTAMINA HULU ROKAN APPROVAL

CHECKED | APPROVED

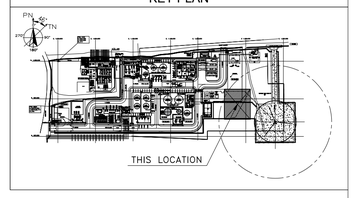PROJECT : JASA PEMBANGUNAN FASILITAS PRODUKSI STASIUN PENGUMPUL (SP) TANJUNG MIRING BARAT & KARANGAN TIMUR

OWNER : skkmigas PERTAMINA EP

CONTRACTOR: POG

| SCALE : | DRAWING NO : | SHEET. NO. | REV |
|---|---|---|---|
| 1:100 | TMBP-SP001-PI-LAY-D111 | 1 OF 1 | A |

DRAWING TITLE :

PIPING LAYOUT AROUND FLARE (STANCHION) AREA