ARCHITECTURE
FLOOR PLAN, ROOF PLAN, & ELEVATION
OF CLOSED DRAIN VESSEL SHELTER

TMBP–SP001–CS–ARC–D112

NOTES :

1. BEFORE STARTING CONSTRUCTION, CONTRACTOR SHALL VERIFY ACTUAL FIELD CONDITION AND DETERMINE LOCATION, ELEVATION OF EXISTING GRADING AND OTHER STRUCTURE. THE CONTRACTOR SHALL TAKE NECESSARY MEASURES TO HOLD SAFE AND PREVENT DAMAGE TO ANY EXISTING FACILITIES.

DRAWING REFERENCE	DESCRIPTION	REV	DATE	DESCRIPTION	PREPR'D	CHECK'D	APRV'D	CHECKED	APPROVED
		A	12–01–2026	ISSUED FOR REVIEW	NAS	AS	MR	YR	MRZ/RS

PT. PERTAMINA EP APPROVAL

PROCET :

JASA PEMBANGUNAN FASILITAS PRODUKSI STASIUN PENGUMPUL (SP) TANJUNG MIRING BARAT & KARANGAN TIMUR

OWNER :

skkmigas PERTAMINA EP

CONTRACTOR :

POG

SCALE :	DRAWING NO.	SHEET. NO.	REV
NTS	TMBP–SP001–CS–ARC–D112	1 OF 2	A

DRAWING TITLE :

ARCHITECTURE
FLOOR PLAN, ROOF PLAN, & ELEVATION
OF CLOSED DRAIN VESSEL SHELTER

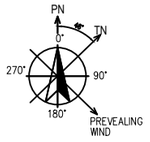

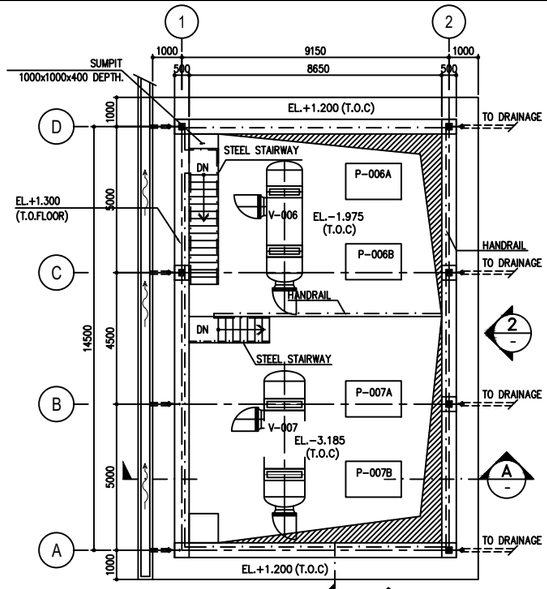

FLOOR PLAN
SCALE 1:100

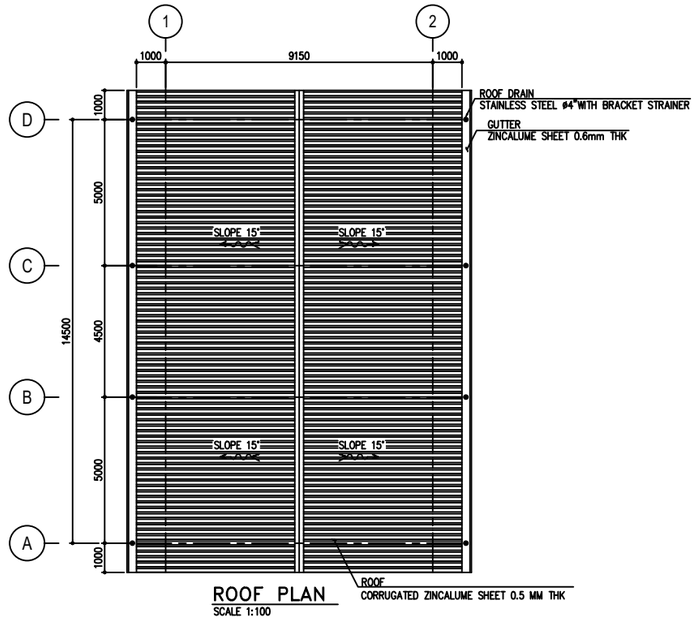

ROOF PLAN
SCALE 1:100

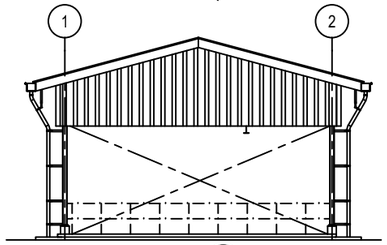

VIEW 1
SCALE: 1 : 100

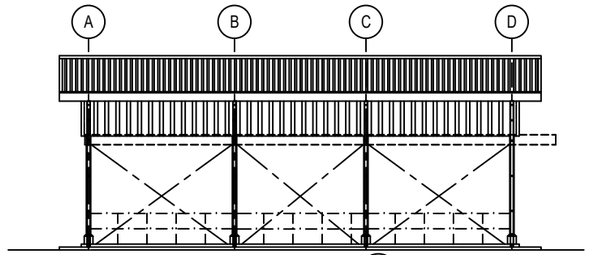

VIEW 2
SCALE: 1 : 100

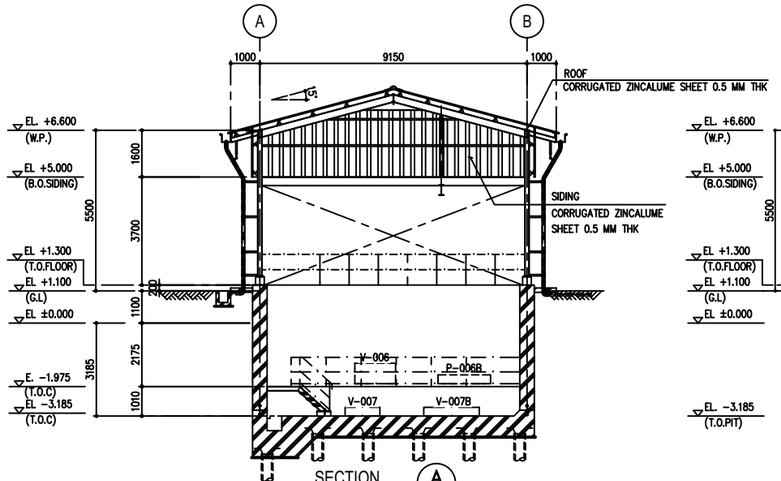

SECTION A
SCALE: 1 : 100

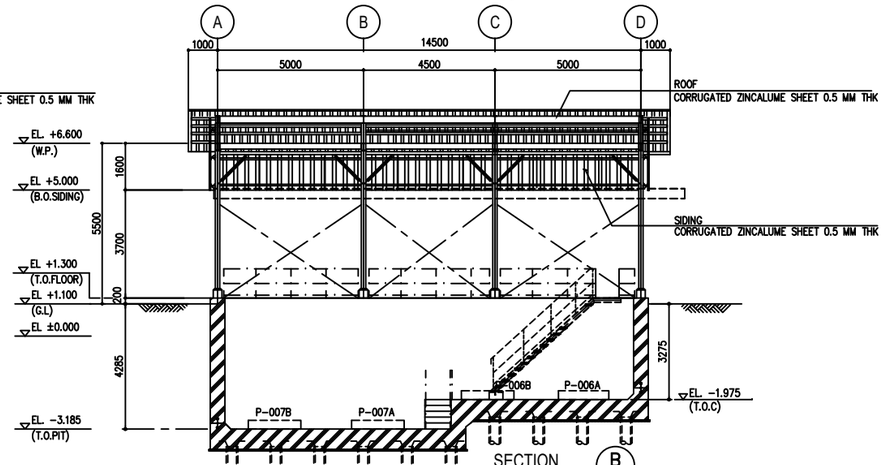

SECTION B
SCALE: 1 : 100

KEY PLAN

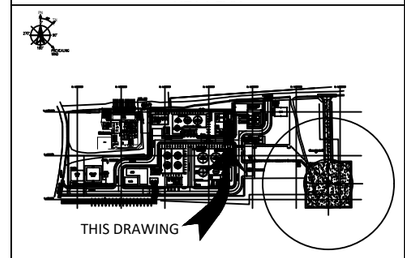

CATATAN

NOTE :
1. ALL DIMENSION AND ELEVATION ARE IN MILLIMETERS, UNLESS OTHERWISE NOTED.
2. REFERENCE OF ELEVATION: EL = 0,00 = MSL+33.75 = EL.+1.100
3. LEGEND :
   - = REINFORCED CONCRETE
   - = BRICK WALL
   - = SLOPE
4. THIS SHELTER INCLUDE MANUAL HOIST CRANE 3 TON
5. ABBREVIATION :
   G.L = GROUND LEVFL
   F.F.L = FLOOR FINISH LEVFL
   E.L = ELEVATION LEVFL
   T.O.C = TOP OF CONCRETE

FINISHING SCHEDULE

SURFACE OR PART OF	MATERIAL	FINISH	REMARK
ROOF	CORRUGATED ZINCALUME SHEET 0.5 MM THK (BMT)	PVF2 PLUS, COLOR: LATER	–
SIDING	CORRUGATED ZINCALUME SHEET 0.5 MM THK (BMT)	PVF2 PLUS, COLOR: LATER	–
FLASHING AND GUTTER	FLAT ZINCALUME SHEET 0.6 MM THK (BMT)	PVF2 PLUS, COLOR: LATER	–
ROOF EAVES	FLAT ZINCALUME SHEET 0.6 MM THK (BMT)	PVF2 PLUS, COLOR: LATER	–
FLOOR AND OUT DOOR STEP	REINFORCED CONCRETE	STEEL TROWEL FINISH	–
DOWNSPOUT	PVC PIPE ø4" AW CLASS, WITH DOWNSPOUT FIXING GALVANIZED PLATE BAR 4 THK @1200	PAINTED	–
ROOF DRAIN	STAINLESS STEEL ø4" W/ BRACKET STRAINER	–	–
HANDRAIL	STEEL GALVANIZED PIPE ø2"	STEEL PAINTED	–

STRUCTURE

COLUMN	STEEL STRUCTURE	PAINTED	–
ROOF FRAME	STEEL STRUCTURE	PAINTED	–
FOUNDATION	REINFORCED CONCRETE	–	–

NOTES :
1. BEFORE STARTING CONSTRUCTION, CONTRACTOR SHALL VERIFY ACTUAL FIELD CONDITION AND DETERMINE LOCATION, ELEVATION OF EXISTING GRADING AND OTHER STRUCTURE. THE CONTRACTOR SHALL TAKE NECESSARY MEASURES TO HOLD SAFE AND PREVENT DAMAGE TO ANY EXISTING FACILITIES.

DRAWING REFERENCE	DESCRIPTION	REV	DATE	DESCRIPTION	PREPR'D	CHECK'D	APRV'D	CHECKED	APPROVED
TMBP-SP001-CS-BLD-D110	FOUNDATION PLAN, DETAIL AND SECTION OF CLOSED DRAIN VESSEL AND KNOCK OUT DRUM VESSEL SHELTER								
TMBP-SP001-CS-FRM-D111	FRAMING PLAN, ROOF PLAN, ELEVATION, SECTION & DETAIL OF CLOSED DRAIN VESSEL AND KNOCK OUT DRUM VESSEL SHELTER								
TMBP-SP001-PI-PLP-101	OVERALL PLOT PLAN DRAWING	A	12-01-2026	ISSUED FOR REVIEW	NAS	AS	MR	YR	MRZ/RS

PT. PERTAMINA EP APPROVAL

PROCET :
JASA PEMBANGUNAN FASILITAS PRODUKSI STASIUN PENGUMPUL (SP) TANJUNG MIRING BARAT & KARANGAN TIMUR

OWNER : skkmigas PERTAMINA EP

CONTRACTOR : POG

SCALE : 1 : 100

DRAWING NO. TMBP-SP001-CS-ARC-D112

SHEET. NO. 2 OF 2

REV A

DRAWING TITLE :
ARCHITECTURE
FLOOR PLAN, ROOF PLAN, & ELEVATION
OF CLOSED DRAIN VESSEL SHELTER