GENERAL LAYOUT DRAWING UNDERGROUND COMPOSITE

TMBP-SP001-CS-LAY-D106

NOTES :

DRAWING REFERENCE	DESCRIPTION	REV	DATE	DESCRIPTION	PREPR'D	CHECK'D	APRV'D	CHECKED	APPROVED
		A	13-01-2026	ISSUED FOR REVIEW	NAS	AS	MR	YR	MRZ/RS

PT. PERTAMINA EP APPROVAL

PROCET :

JASA PEMBANGUNAN FASILITAS PRODUKSI STASIUN PENGUMPUL (SP)
TANJUNG MIRING BARAT & KARANGAN TIMUR

OWNER :

skkmigas PERTAMINA EP

CONTRACTOR :

POG

SCALE :	DRAWING NO.	SHEET. NO.	REV
NTS	TMBP-SP001-CS-LAY-D106	1 OF 1	A

DRAWING TITLE :

GENERAL LAYOUT DRAWING UNDERGROUND COMPOSITE

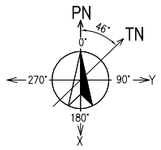

KEY PLAN

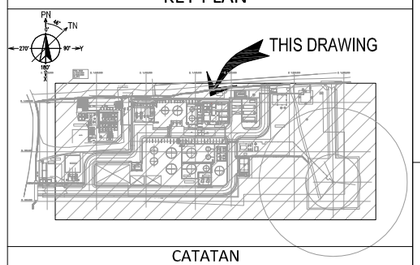

CATATAN

NOTE :

1. ALL DIMENSIONS ARE IN MILLIMETERS, ELEVATION AND COORDINATE ARE IN METERS UNLESS OTHERWISE NOTED.
2. REFERENCE OF ELEVATION AND COORDINATE
   GL. ± 0.000 = MSL+ 19.000 = EL +1.100
   PE = 1.000.000 : E = 424962.745
   PN = 1.000.000 : N = 9607576.210

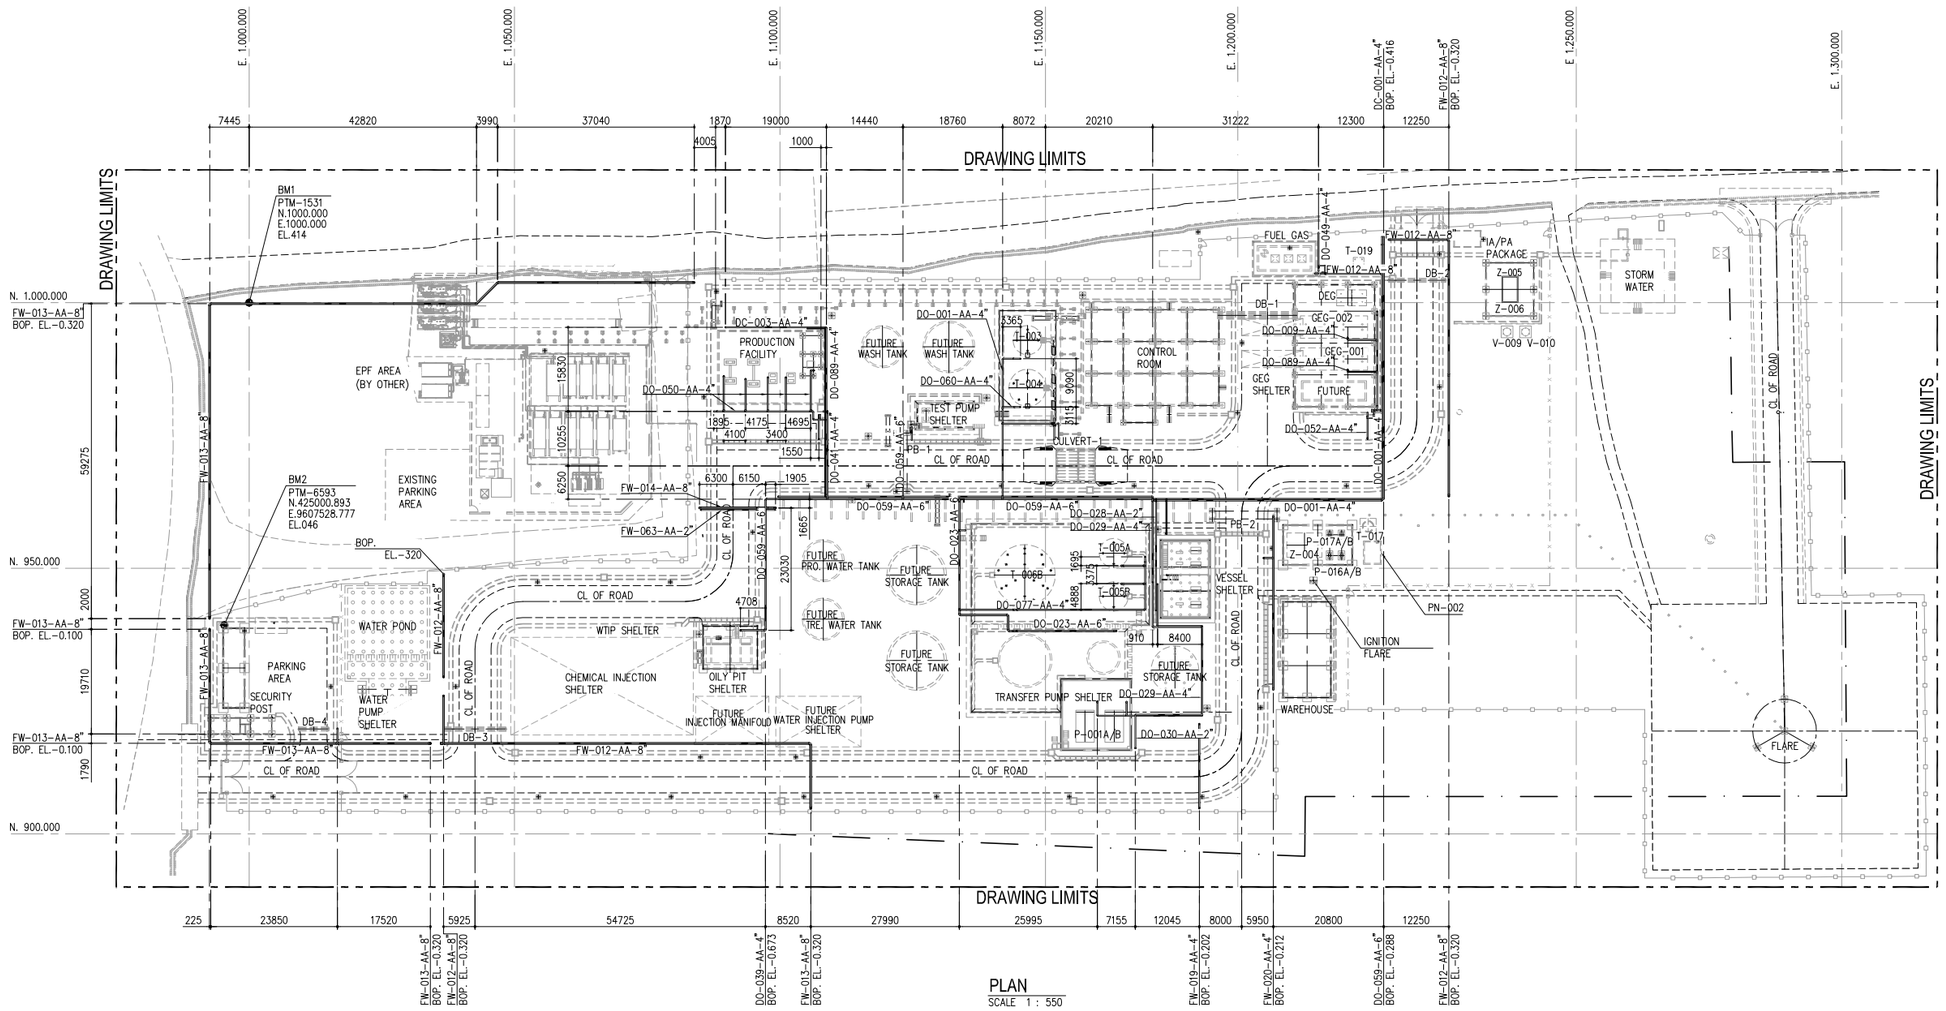

PLAN
SCALE 1 : 550

NOTES :

1. BEFORE STARTING CONSTRUCTION, CONTRACTOR SHALL VERIFY ACTUAL FIELD CONDITION AND DETERMINE LOCATION, ELEVATION OF EXISTING GRADING AND OTHER STRUCTURE. THE CONTRACTOR SHALL TAKE NECESSARY MEASURES TO HOLD SAFE AND PREVENT DAMAGE TO ANY EXISTING FACILITIES.

DRAWING REFERENCE	DESCRIPTION	REV	DATE	DESCRIPTION	PREPR'D	CHECK'D	APRV'D	CHECKED	APPROVED
TMBP-SP001-PI-LAY-D117	PIPING LAYOUT UNDER GROUND LINE FOR FIRE WATER MAIN RING AND CLOSED / OPEN DRAIN								
TMBP-SP001-CS-LAY-D102	OVERALL FOUNDATION LAYOUT								
TMBP-SP001-PI-PLP-D101	OVERALL PLOT PLAN DRAWING	A	13-01-2026	ISSUED FOR REVIEW	NAS	AS	MR	YR	MRZ/RS

PT. PERTAMINA EP APPROVAL

PROCET :
JASA PEMBANGUNAN FASILITAS PRODUKSI STASIUN PENGUMPUL (SP) TANJUNG MIRING BARAT & KARANGAN TIMUR

OWNER : skkmigas PERTAMINA EP

CONTRACTOR : POG

SCALE :	DRAWING NO.	SHEET. NO.	REV
1 : 550	TMBP-SP001-CS-LAY-D106	1 OF 1	A

DRAWING TITLE :

GENERAL LAYOUT DRAWING UNDERGROUND COMPOSITE