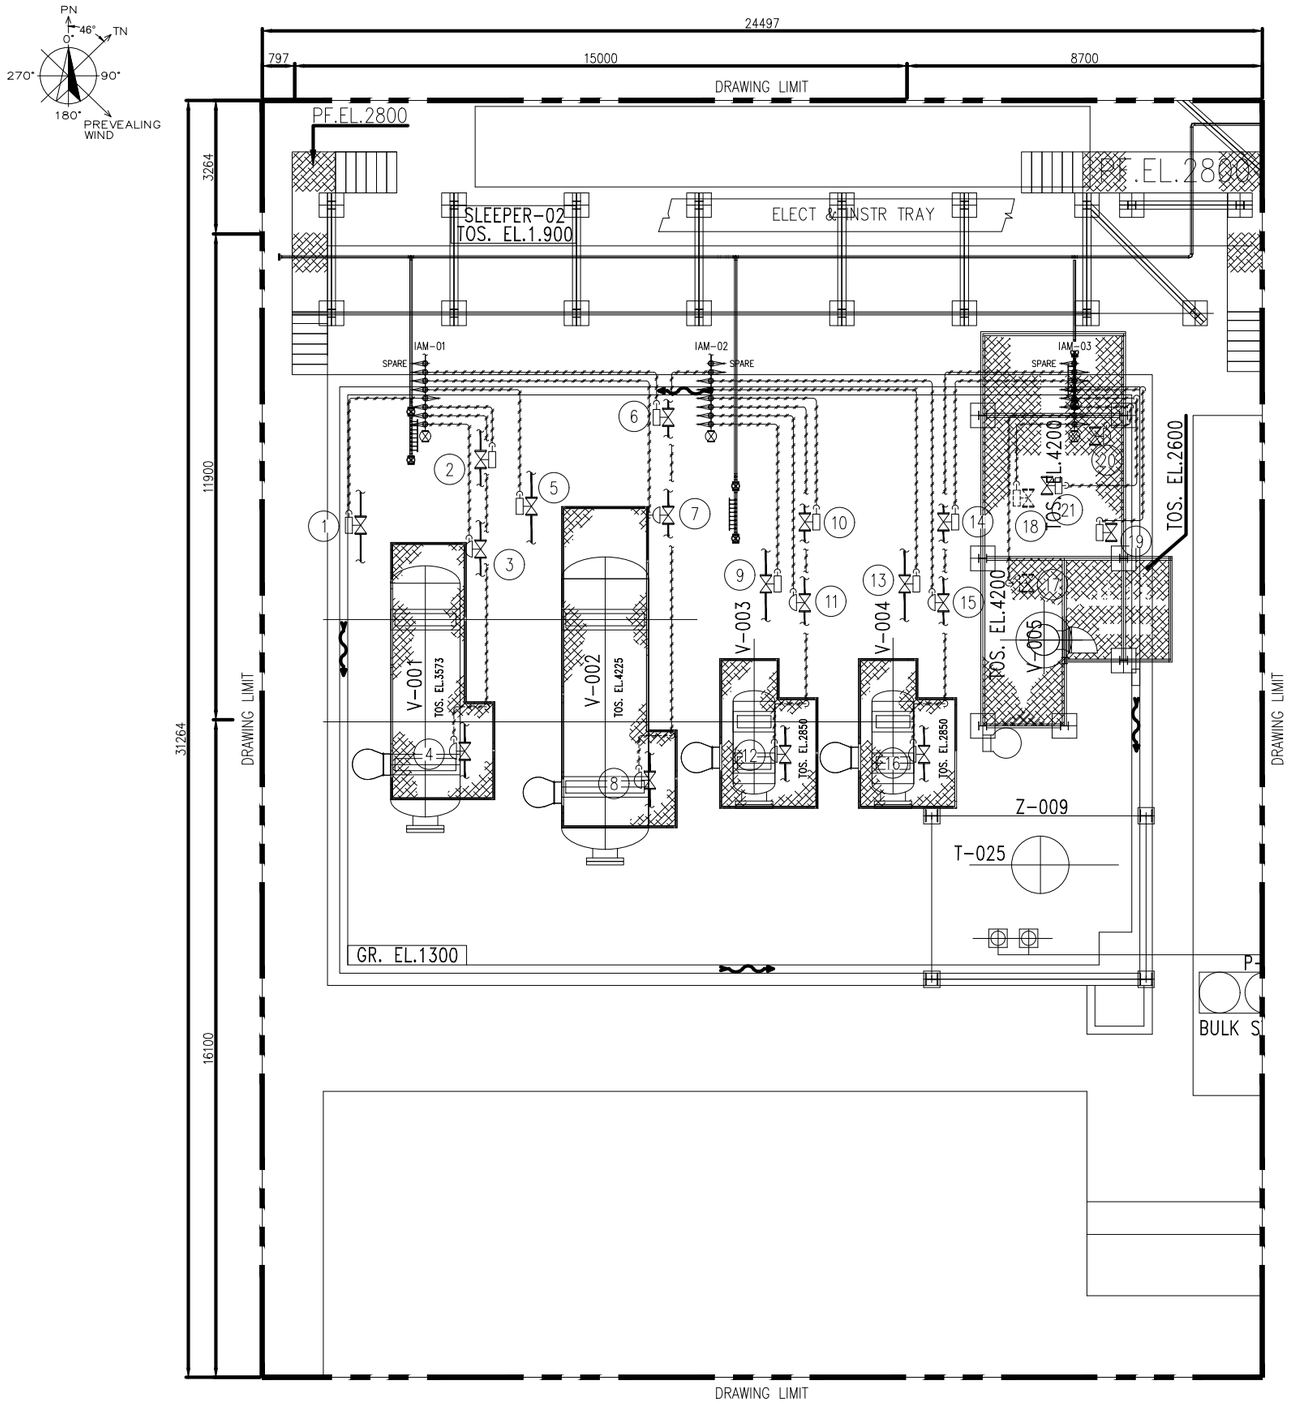

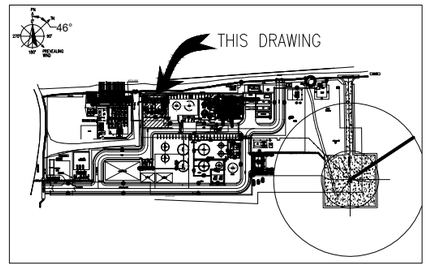

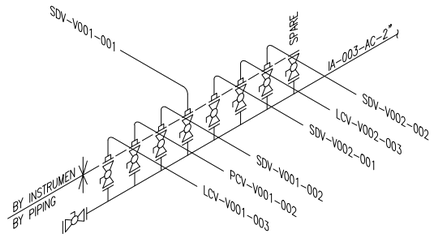

INSTRUMENT AIR MANIFOLD (IAM) – 01

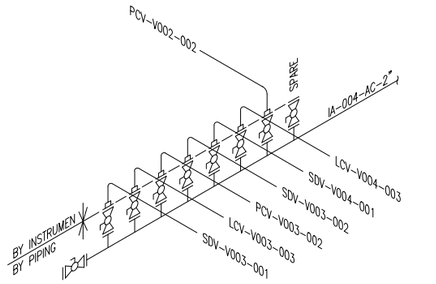

INSTRUMENT AIR MANIFOLD (IAM) – 02

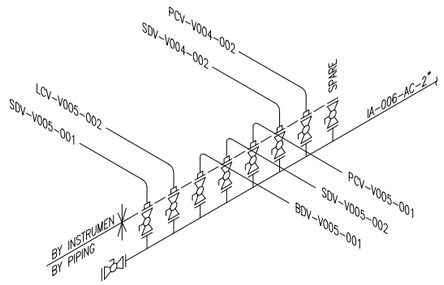

INSTRUMENT AIR MANIFOLD (IAM) – 03

SIMBOL & KETERANGAN	
SIMBOL	KETERANGAN
	PNEUMATIC TUBE
	SHUTDOWN VALVE (SDV, BDV)
	CONTROL VALVE (FCV, PCV, LCP)
	AIR SUPPLY HEADER

INSTRUMENT EQUIPMENT LIST

NO	TAG NO	IAM NO.	PID NO.	LOCATION	REMARKS
01	SDV-V001-001	IAM-01	TMBP-SP001-PR-PID-D101	F-2	
02	SDV-V001-002	IAM-01	TMBP-SP001-PR-PID-D101	F-2	
03	LCV-V001-003	IAM-01	TMBP-SP001-PR-PID-D101	F-3	
04	PCV-V001-002	IAM-01	TMBP-SP001-PR-PID-D101	E-2	
05	SDV-V002-001	IAM-01	TMBP-SP001-PR-PID-D102	F-3	
06	SDV-V002-002	IAM-01	TMBP-SP001-PR-PID-D102	F-3	
07	LCV-V002-003	IAM-01	TMBP-SP001-PR-PID-D102	F-3	
08	PCV-V002-002	IAM-02	TMBP-SP001-PR-PID-D102	E-3	
09	SDV-V003-001	IAM-02	TMBP-SP001-PR-PID-D101	F-4	
10	SDV-V003-002	IAM-02	TMBP-SP001-PR-PID-D101	F-4	
11	LCV-V003-003	IAM-02	TMBP-SP001-PR-PID-D101	E-4	
12	PCV-V003-002	IAM-02	TMBP-SP001-PR-PID-D101	E-4	
13	SDV-V004-001	IAM-02	TMBP-SP001-PR-PID-D102	F-4	
14	SDV-V004-002	IAM-03	TMBP-SP001-PR-PID-D102	F-5	
15	LCV-V004-003	IAM-02	TMBP-SP001-PR-PID-D102	F-5	
16	PCV-V004-002	IAM-03	TMBP-SP001-PR-PID-D102	E-4	
17	LCV-V005-002	IAM-03	TMBP-SP001-PR-PID-D114	F-5	
18	SDV-V005-001	IAM-03	TMBP-SP001-PR-PID-D114	F-5	
19	PCV-V005-001	IAM-03	TMBP-SP001-PR-PID-D114	F-5	
20	BDV-V005-001	IAM-03	TMBP-SP001-PR-PID-D114	F-5	
21	SDV-V005-002	IAM-03	TMBP-SP001-PR-PID-D114	F-5	

METERS 0 0.5 1 1.5 2 3 4 5 6 7.5

BAR SCALE 1:75

NOTES :

1. ALL DIMENSIONS ARE IN MILLIMETER, UNLESS NOTED OTHERWISE.
2. FINISH GROUND LEVEL EL = 0,00 = MSL+19.000
3. EPC CONTRACTOR IS RESPONSIBLE FOR VERIFICATION OF THE PLOT PLAN, IF THERE ARE DIFFERENCES, THERE SHOULD BE ASKED AND CLARIFIED

DRAWING REFERENCE	DESCRIPTION	REV	DATE	DESCRIPTION	PREPR'D	CHECK'D	APRV'D	CHECKED	APPROVED
TMBP-SP001-PI-PLP-D101	OVERALL PLOT PLAN								
TMBP-SP001-PR-PID-D114	P&ID FOR PRODUCTION SCRUBBER (V-005)								
TMBP-SP001-PR-PID-D113	P&ID FOR TREATED WATER TANK (T-008) & INJECTION PUMP (P-005 A/B)								
TMBP-SP001-PR-PID-D108	P&ID FOR PRODUCEED WATER TANK (T-007) & FEED WATER PUMP (P-004 A/B)								
TMBP-SP001-PR-PID-D102	P&ID FOR PRODUCTION SEPARATOR KRG (V-002) & TEST SEPARATOR KRG (V-004)								
TMBP-SP001-PR-PID-D101	P&ID FOR PRODUCTION SEPARATOR TMB (V-001) & TEST SEPARATOR TMB (V-003)								
TMBP-SP001-IN-HUP-D109	HOOK UP DRAWING	A	14/01/2026	ISSUED FOR REVIEW	MHP	AS	MR		

PT. PERTAMINA EP APPROVAL

PROJECT : JASA PEMBANGUNAN FASILITAS PRODUKSI STASIUN PENGUMPUL (SP) TANJUNG MIRING BARAT & KARANGAN TIMUR

OWNER : skkmigas PERTAMINA EP

CONTRACTOR : PCG

SCALE : 1:75

DRAWING NO. TMBP – SP001 – IN – LAY – D107

SHEET. NO. 1 OF 1

REV A

DRAWING TITLE : INSTRUMENT AIR DISTRIBUTION DRAWING