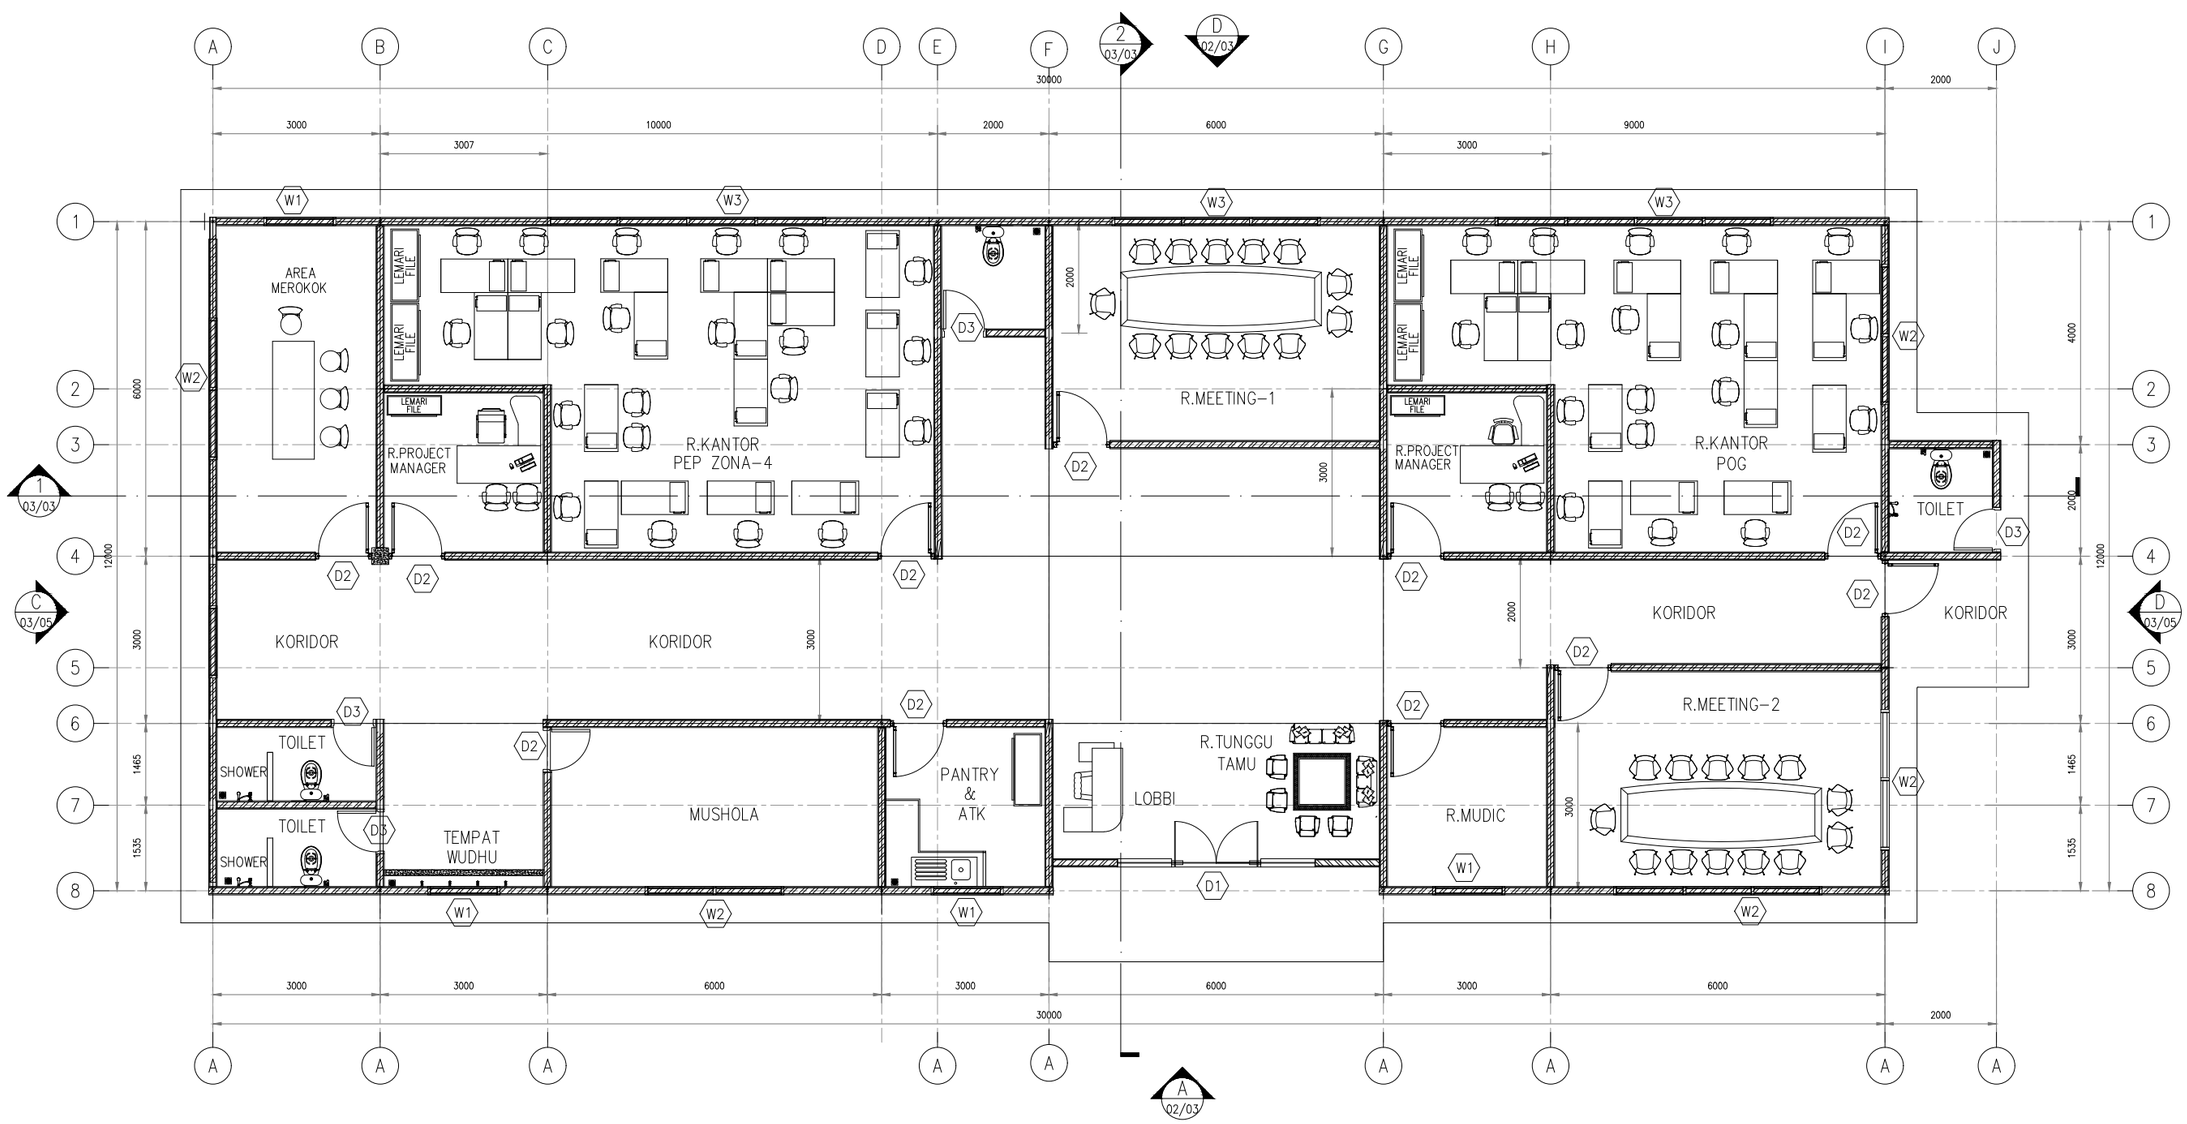

PLAN OFFICE

SKALA: 1:110

NOTES :

DRAWING REFERENCE	DESCRIPTION	REV	DATE	DESCRIPTION	PREPR'D	CHECK'D	APRV'D	CHECKED	APPROVED
		A	30-12-2025	ISSUED FOR REVIEW	NSR	AS	RTN		

PT. PERTAMINA EP APPROVAL

PROCET :

JASA PEMBANGUNAN FASILITAS PRODUKSI STASIUN PENGUMPUL (SP) TANJUNG MIRING BARAT & KARANGAN TIMUR

OWNER : skkmigas PERTAMINA EP

CONTRACTOR : POG

SCALE :	DRAWING NO.	SHEET. NO.	REV
NTS	TMBP – SP001 – CS – DET – D108	01 OF 05	A

DRAWING TITLE :

DRAWING FOR OFFICE

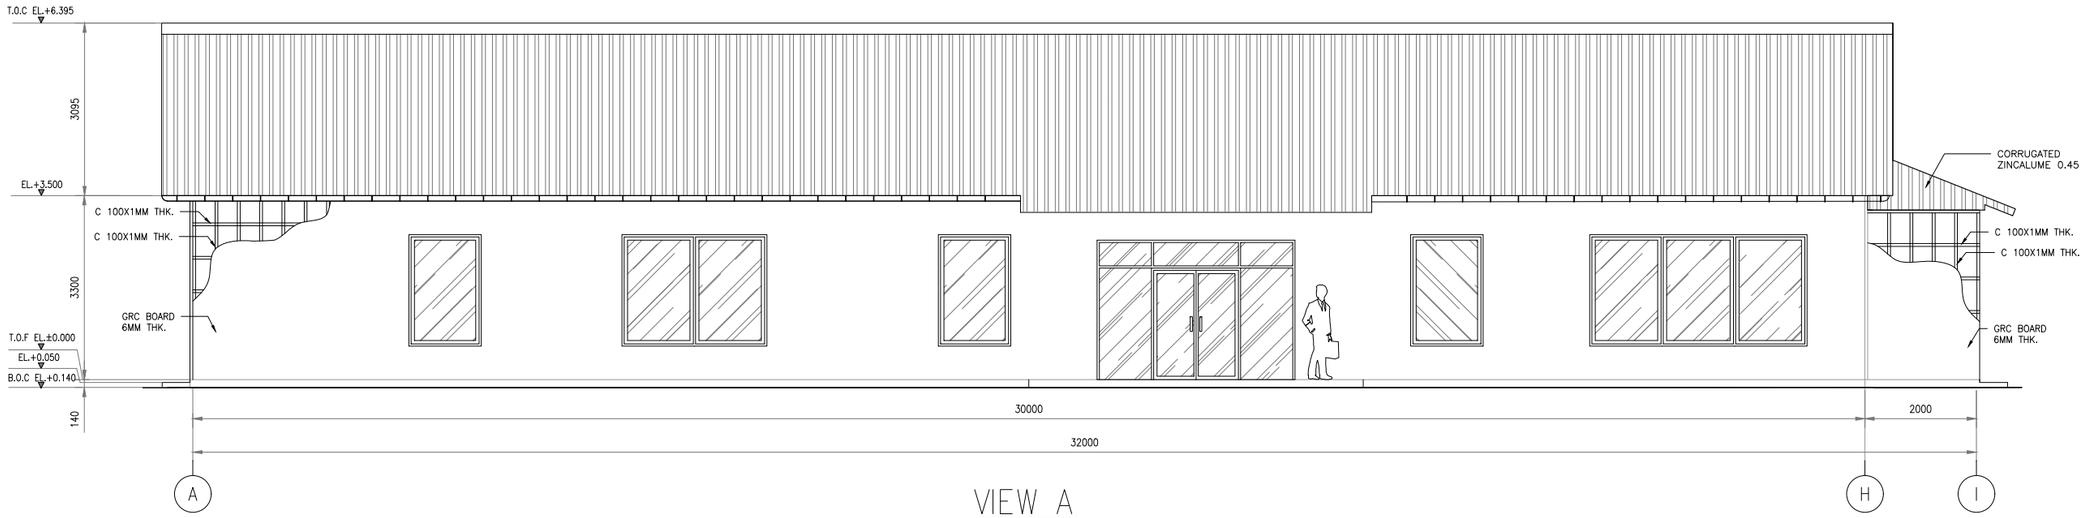

VIEW A

SKALA: 1:110

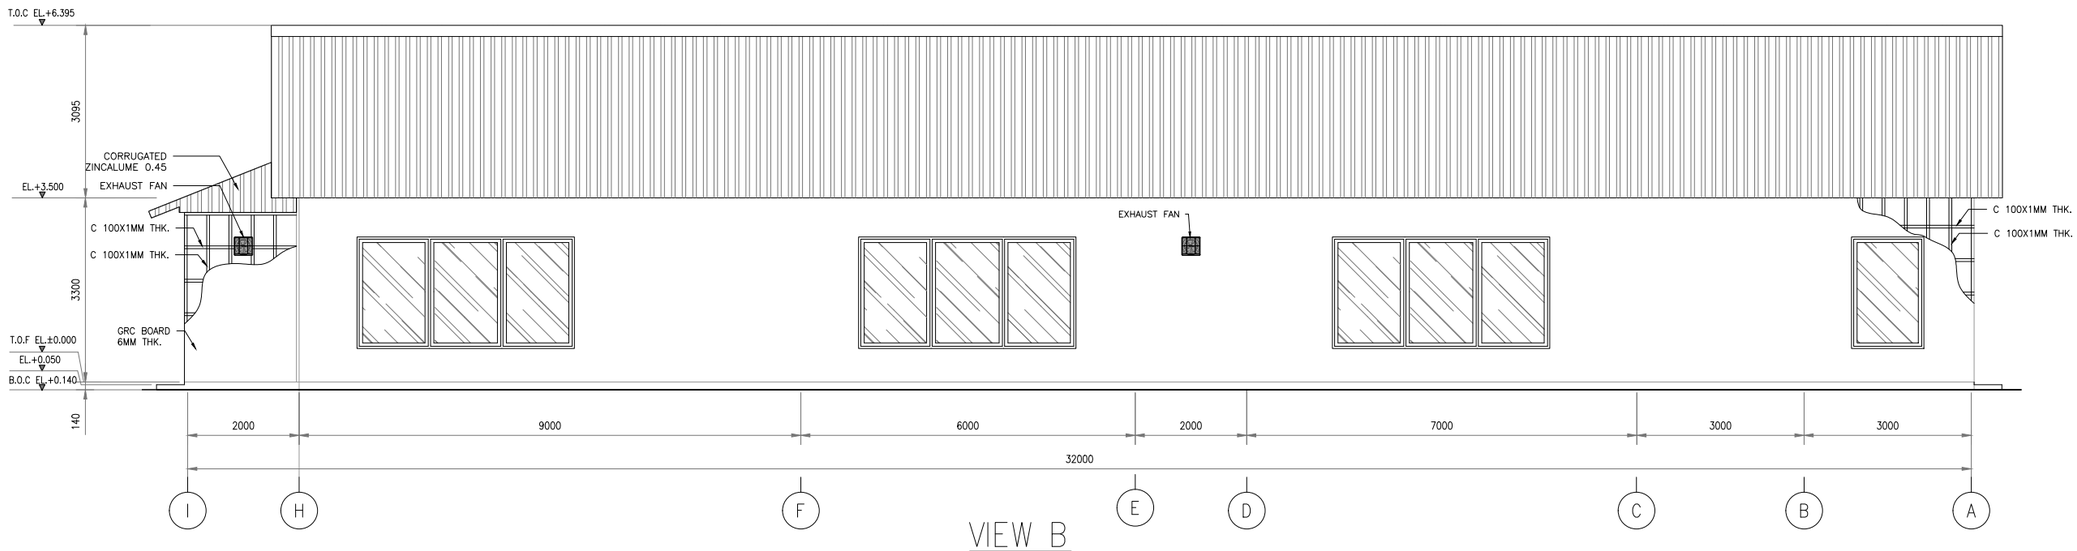

VIEW B

SKALA: 1:110

NOTES :

DRAWING REFERENCE	DESCRIPTION	REV	DATE	DESCRIPTION	PREPR'D	CHECK'D	APRV'D	CHECKED	APPROVED
		A	30-12-2025	ISSUED FOR REVIEW	NSR	AS	RTN		

PT. PERTAMINA EP APPROVAL

PROCET :

JASA PEMBANGUNAN FASILITAS PRODUKSI STASIUN PENGUMPUL (SP)
TANJUNG MIRING BARAT & KARANGAN TIMUR

OWNER : skkmigas PERTAMINA EP

CONTRACTOR : POG

SCALE :	DRAWING NO.	SHEET. NO.	REV
NTS	TMBP – SP001 – CS – DET – D108	02 OF 05	A

DRAWING TITLE :

DRAWING FOR OFFICE

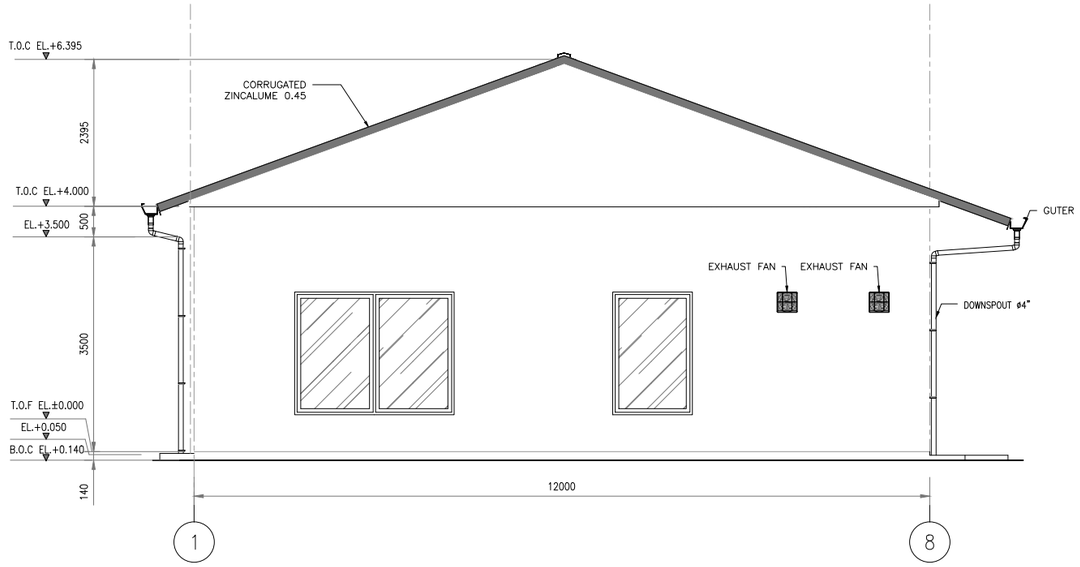

VIEW C
SKALA: 1:100

VIEW D
SKALA: 1:100

NOTES :

DRAWING REFERENCE	DESCRIPTION	REV	DATE	DESCRIPTION	PREPR'D	CHECK'D	APRV'D	CHECKED	APPROVED
		A	30-12-2025	ISSUED FOR REVIEW	NSR	AS	RTN		

PT. PERTAMINA EP APPROVAL

PROCET :
JASA PEMBANGUNAN FASILITAS PRODUKSI STASIUN PENGUMPUL (SP)
TANJUNG MIRING BARAT & KARANGAN TIMUR

OWNER : skkmigas PERTAMINA EP

CONTRACTOR : POG

SCALE :	DRAWING NO.	SHEET. NO.	REV
NTS	TMBP – SP001 – CS – DET – D108	03 OF 05	A

DRAWING TITLE :
DRAWING FOR OFFICE

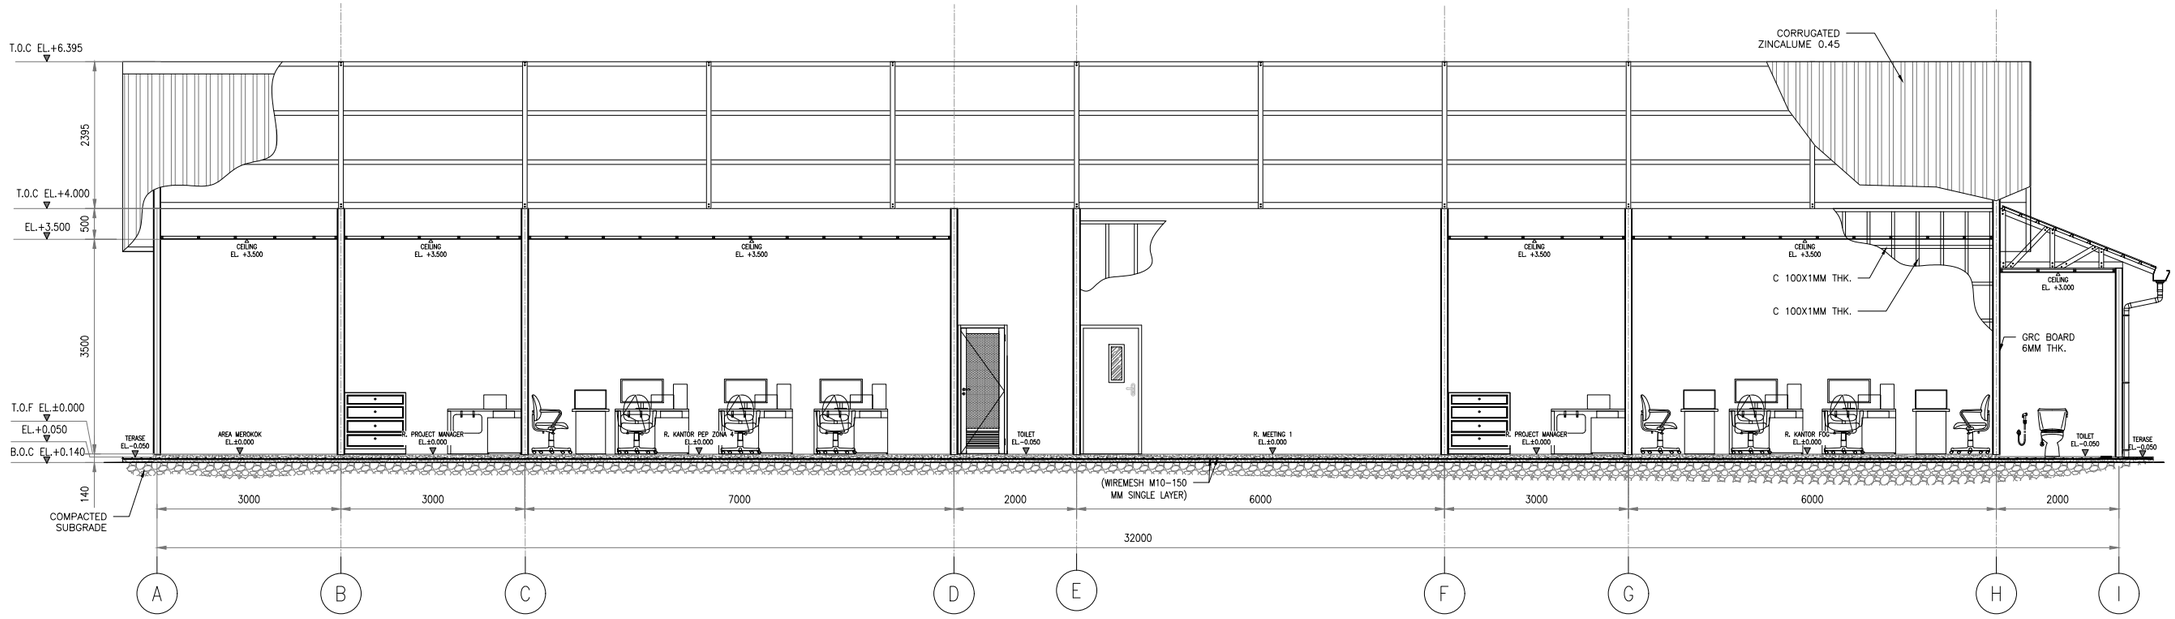

SECTION 1
SKALA: 1:100

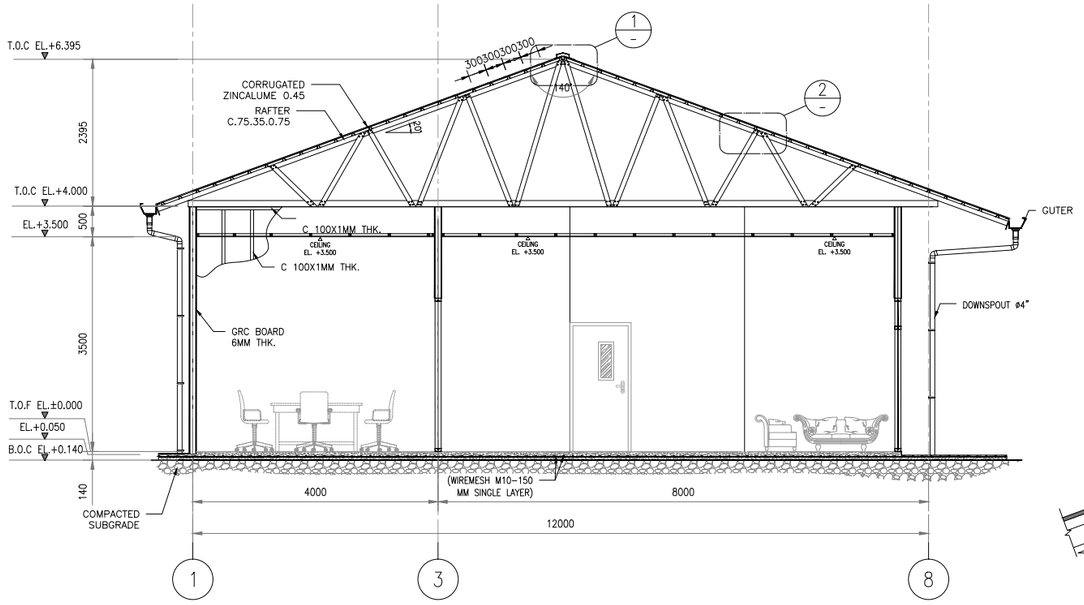

SECTION 2
SKALA: 1:100

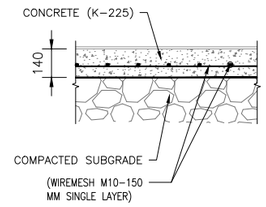

DETAIL FLOOR SLAB
SKALA: 1:30

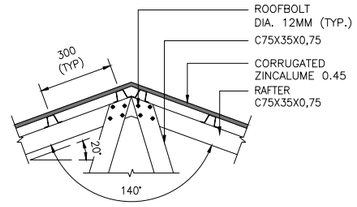

DETAIL 1
SKALA: 1:25

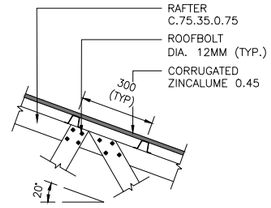

DETAIL 2
SKALA: 1:25

NOTES :

DRAWING REFERENCE	DESCRIPTION	REV	DATE	DESCRIPTION	PREPR'D	CHECK'D	APRV'D	CHECKED	APPROVED
		A	30-12-2025	ISSUED FOR REVIEW	NSR	AS	RTN		

PT. PERTAMINA EP APPROVAL

PROCET : JASA PEMBANGUNAN FASILITAS PRODUKSI STASIUN PENGUMPUL (SP) TANJUNG MIRING BARAT & KARANGAN TIMUR

OWNER : skkmigas PERTAMINA EP

CONTRACTOR : POG

SCALE :	DRAWING NO.	SHEET. NO.	REV
NTS	TMBP – SP001 – CS – DET – D108	04 OF 05	A

DRAWING TITLE : DRAWING FOR OFFICE

WINDOWS SCHEDULE

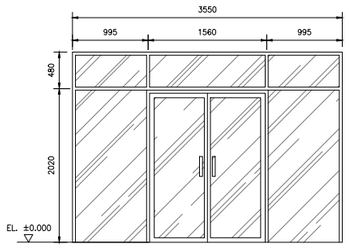

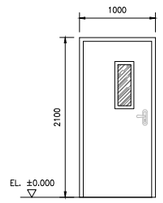

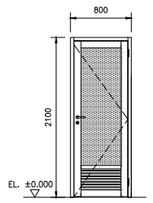

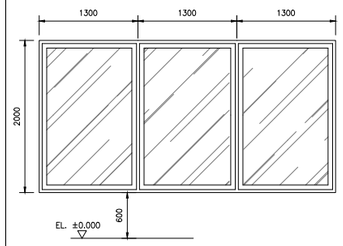

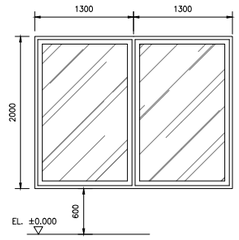

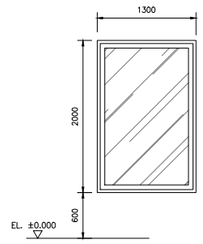

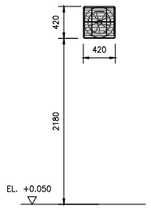

TYPE		D1	TYPE		D2	TYPE		D3	TYPE		W3	TYPE		W2	TYPE		W1	TYPE		
MATERIAL & FINISH	DOOR/WIN. FRAME	ALUMUNIUM FRAME 4 INCH	MATERIAL & FINISH	DOOR/WIN. FRAME	ALUMUNIUM FRAME 4 INCH	MATERIAL & FINISH	DOOR/WIN. FRAME	ALUMUNIUM FRAME 4 INCH	MATERIAL & FINISH	DOOR/WIN. FRAME	ALUMUNIUM FRAME 4 INCH	MATERIAL & FINISH	DOOR/WIN. FRAME	ALUMUNIUM FRAME 4 INCH	MATERIAL & FINISH	DOOR/WIN. FRAME	ALUMUNIUM FRAME 4 INCH	MATERIAL & FINISH	DOOR/WIN. FRAME	ALUMUNIUM FRAME 4 INCH
	DOOR LEAF	ALUMUNIUM WITH GLASS 5MM		DOOR LEAF	DOUBLE TEAKWOOD WITH GLASS 5MM		DOOR LEAF	ALUMUNIUM		DOOR LEAF			DOOR LEAF			DOOR LEAF			DOOR LEAF	
	WINDOW LEAF			WINDOW LEAF			WINDOW LEAF			WINDOW LEAF	ALUMUNIUM WITH GLASS 5MM		WINDOW LEAF	ALUMUNIUM WITH GLASS 5MM		WINDOW LEAF	ALUMUNIUM WITH GLASS 5MM		WINDOW LEAF	
GLASS			GLASS			GLASS			GLASS			GLASS			GLASS			GLASS		
ACCESORIES		1 SET HANDLE	ACCESORIES		1 SET HANDLE	ACCESORIES		1 SET HANDLE	ACCESORIES		1 SET HANDLE	ACCESORIES		1 SET HANDLE	ACCESORIES		1 SET HANDLE	ACCESORIES		
		4 HINGE			2 HINGE			2 HINGE			6 HINGE			4 HINGE			2 HINGE			
		2 DOOR CLOSER			1 DOOR CLOSER			1 SET LOCK CASE			1 SET LOCK CASE			1 SET LOCK CASE			1 SET LOCK CASE			
		1 SET LOCK CASE			1 SET LOCK CASE			PVC LOUVER												
		2 DOOR STOPPER			1 DOOR STOPPER															

INTERIOR FINISH SCHEDULE		
MARK	NAME	MATERIAL/SPECIFICATION
1	FLOOR	CERAMIC TILE 400x400mm
2	WALL	GRC BOARD 6MM THK.
3	CEILING	GYPSUM BOARD 9MM THK.
4	ROOF	CORRUGATED ZINCALUME 0.45

NOTES :

DRAWING REFERENCE	DESCRIPTION	REV	DATE	DESCRIPTION	PREPR'D	CHECK'D	APRV'D	CHECKED	APPROVED
		A	30-12-2025	ISSUED FOR REVIEW	NSR	AS	RTN		

PT. PERTAMINA EP APPROVAL

PROCET :
JASA PEMBANGUNAN FASILITAS PRODUKSI STASIUN PENGUMPUL (SP)
TANJUNG MIRING BARAT & KARANGAN TIMUR

OWNER : skkmigas PERTAMINA EP

CONTRACTOR : POG

SCALE : NTS

DRAWING NO. TMBP – SP001 – CS – DET – D108

SHEET. NO. 05 OF 05

REV A

DRAWING TITLE :
DRAWING FOR OFFICE