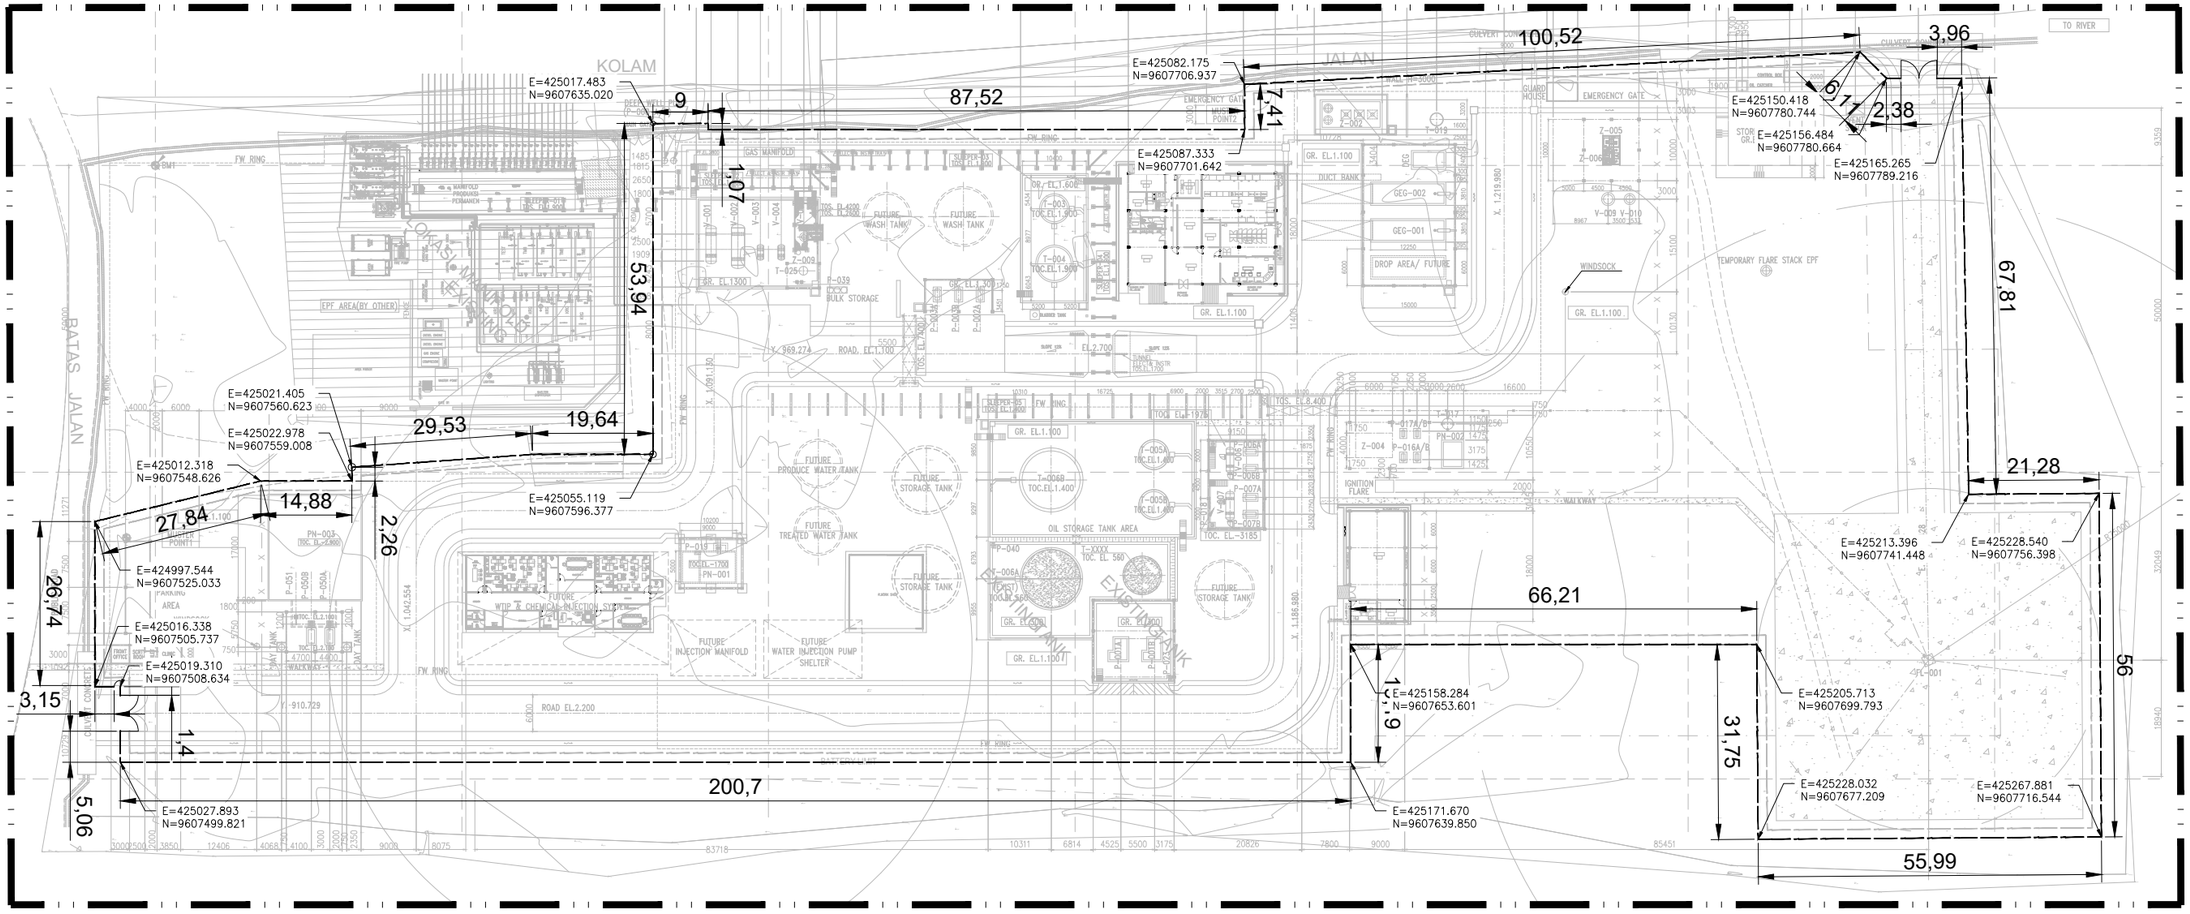

LAYOUT PLAN FENCE & GATE

SKALA: 1:700

NOTES :

DRAWING REFERENCE	DESCRIPTION	REV	DATE	DESCRIPTION	PREPR'D	CHECK'D	APRV'D	CHECKED	APPROVED
		A	30-12-2025	ISSUED FOR REVIEW	NSR	AS	RTN		

PT. PERTAMINA EP APPROVAL

PROCET :

JASA PEMBANGUNAN FASILITAS PRODUKSI STASIUN PENGUMPUL (SP) TANJUNG MIRING BARAT & KARANGAN TIMUR

OWNER :

skkmigas PERTAMINA EP

CONTRACTOR :

POG

SCALE :	DRAWING NO.	SHEET. NO.	REV
NTS	TMBP – SP001 – CS – DET – D110	01 OF 02	A

DRAWING TITLE :

DRAWING FOR FENCE & GATE

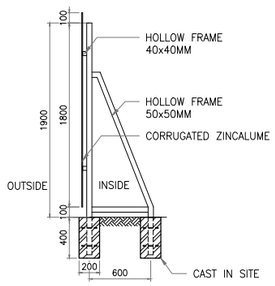

SECTION 1
SKALA: 1:60

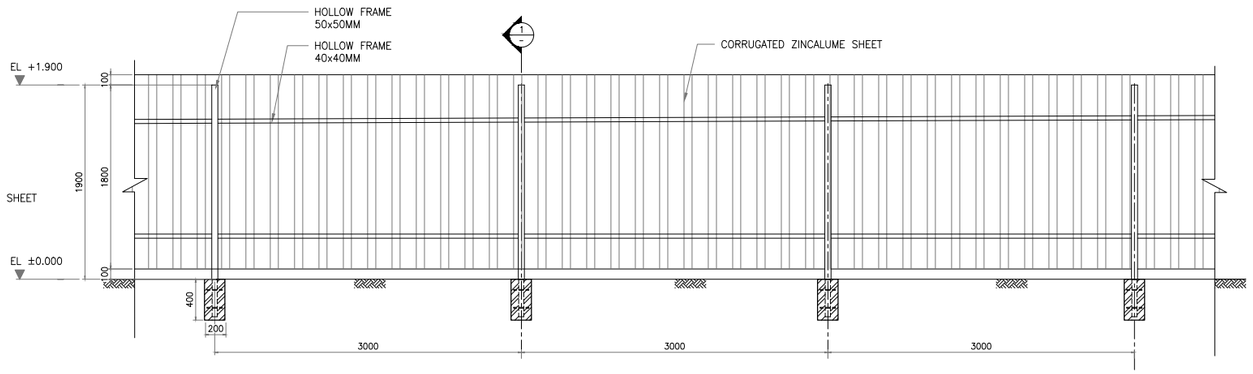

VIEW FENCE
SKALA: 1:60

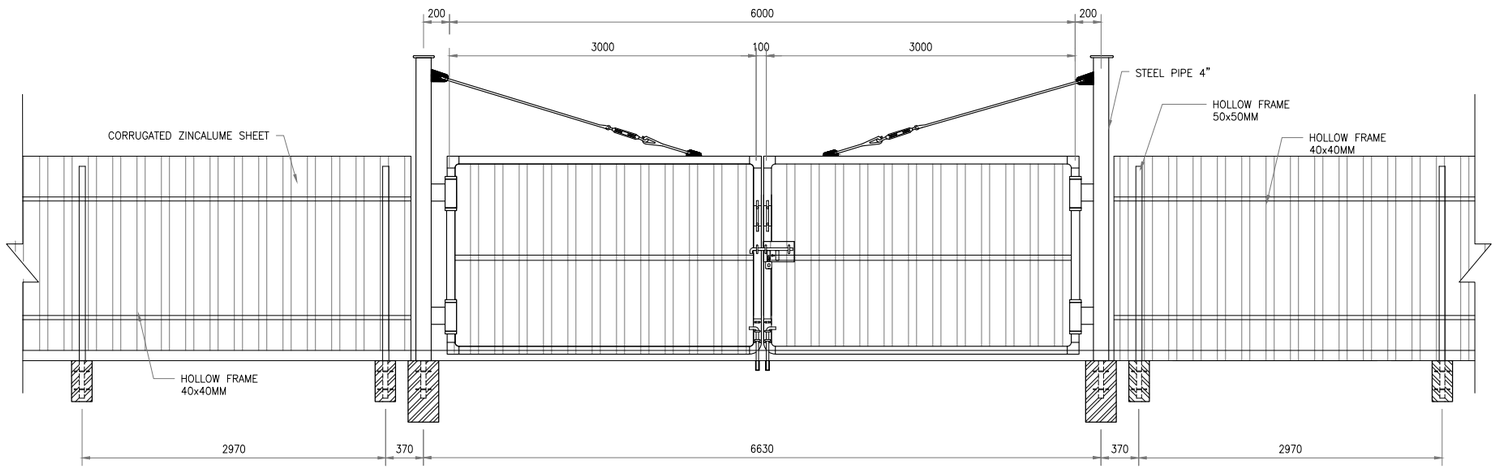

VIEW GATE
SKALA: 1:60

NOTES :

DRAWING REFERENCE	DESCRIPTION	REV	DATE	DESCRIPTION	PREPR'D	CHECK'D	APRV'D	CHECKED	APPROVED
		A	30-12-2025	ISSUED FOR REVIEW	NSR	AS	RTN		

PT. PERTAMINA EP APPROVAL

PROCET :
JASA PEMBANGUNAN FASILITAS PRODUKSI STASIUN PENGUMPUL (SP)
TANJUNG MIRING BARAT & KARANGAN TIMUR

OWNER : skkmigas PERTAMINA EP

CONTRACTOR : POG

SCALE :	DRAWING NO.	SHEET. NO.	REV
NTS	TMBP – SP001 – CS – DET – D110	02 OF 02	A

DRAWING TITLE :
DRAWING FOR FENCE & GATE