FOUNDATION PLAN OF PIPE SLEEPER

TMBP-SP001-CS-FDN-D115

NOTES :

1. BEFORE STARTING CONSTRUCTION, CONTRACTOR SHALL VERIFY ACTUAL FIELD CONDITION AND DETERMINE LOCATION, ELEVATION OF EXISTING GRADING AND OTHER STRUCTURE. THE CONTRACTOR SHALL TAKE NECESSARY MEASURES TO HOLD SAFE AND PREVENT DAMAGE TO ANY EXISTING FACILITIES.

DRAWING REFERENCE	DESCRIPTION	REV	DATE	DESCRIPTION	PREPR'D	CHECK'D	APRV'D	CHECKED	APPROVED
		A	12-01-2026	ISSUED FOR REVIEW	NAS	AS	MR	YR	MRZ/RS

PT. PERTAMINA EP APPROVAL

PROCET :

JASA PEMBANGUNAN FASILITAS PRODUKSI STASIUN PENGUMPUL (SP) TANJUNG MIRING BARAT & KARANGAN TIMUR

OWNER :

skkmigas PERTAMINA EP

CONTRACTOR :

POG

SCALE :	DRAWING NO.	SHEET. NO.	REV
NTS	TMBP-SP001-CS-FDN-D115	1 OF 2	A

DRAWING TITLE :

FOUNDATION PLAN OF PIPE SLEEPER

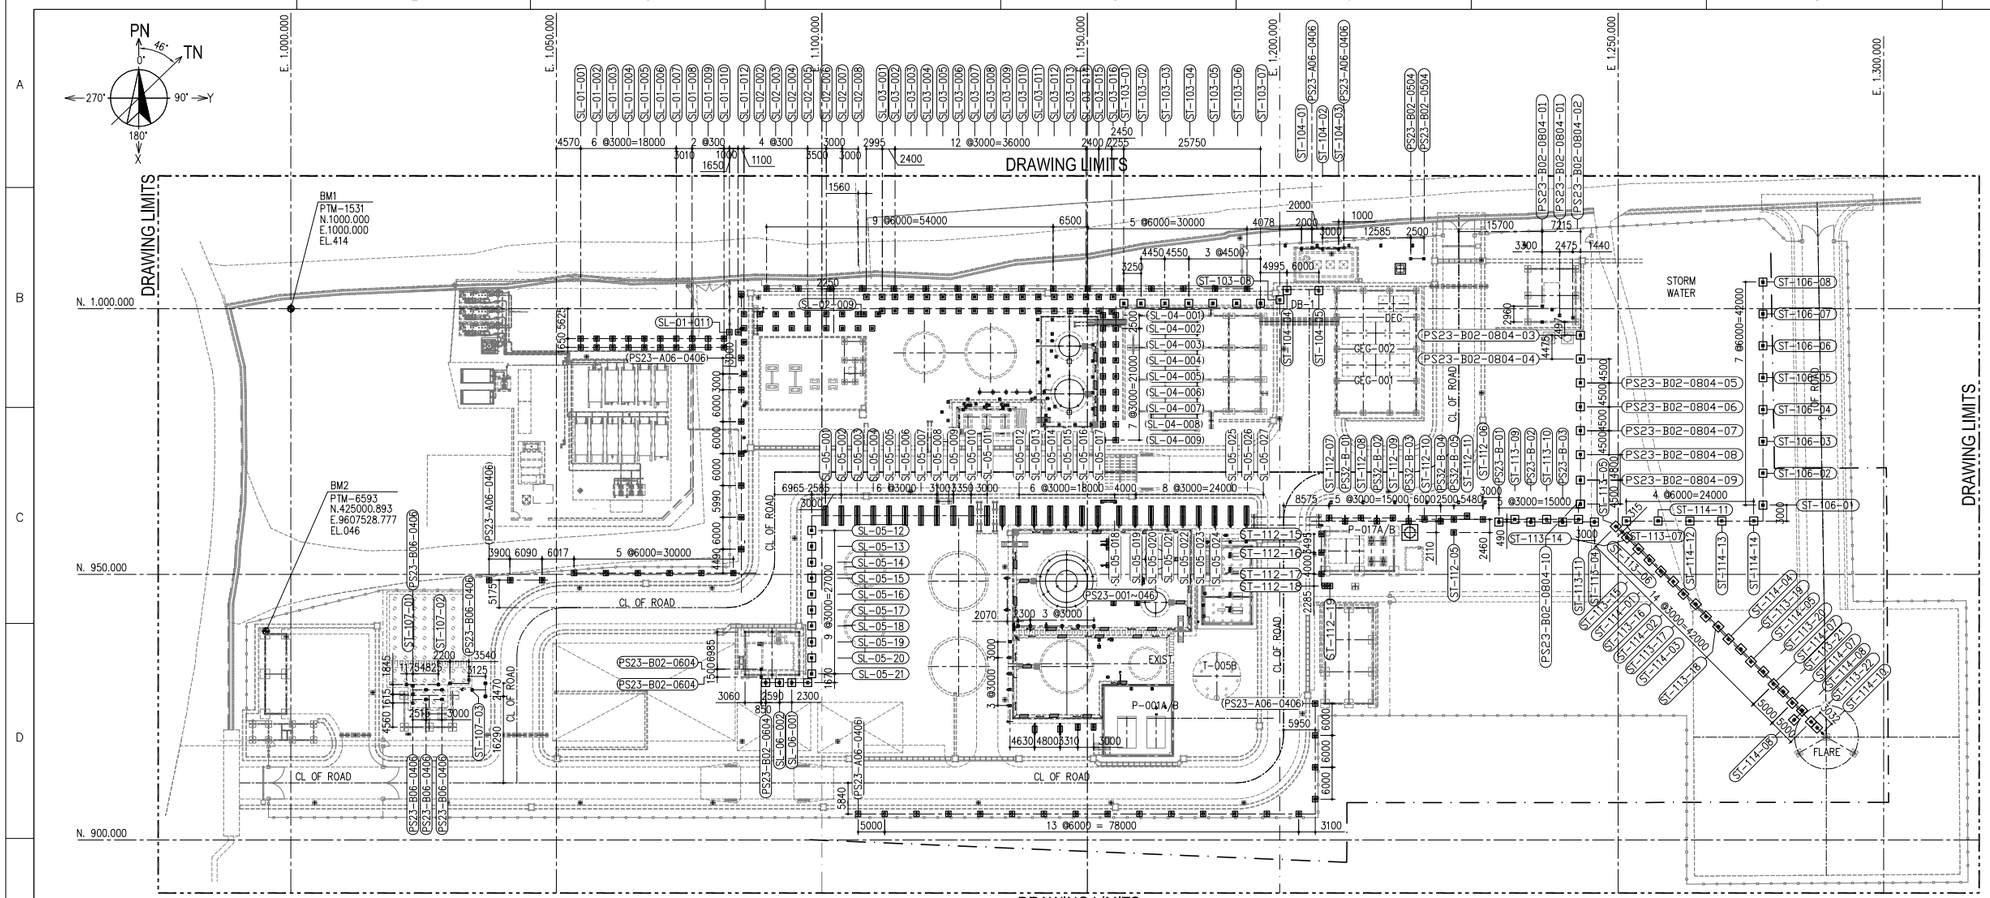

KEY PLAN

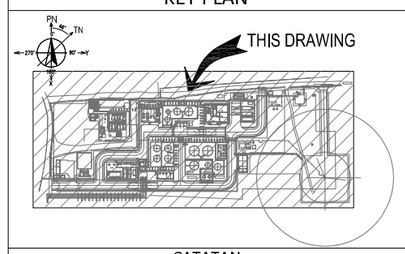

CATATAN

NOTE :

1. ALL DIMENSIONS ARE IN MILLIMETERS, ELEVATION AND COORDINATE ARE IN METERS UNLESS OTHERWISE NOTED.
2. REFERENCE OF ELEVATION AND COORDINATE
   GL. ±0.000 = EL. +33.75 = EL. +1.100
   PE = 1.000.000 : X = 424.965
   PN = 1.000.000 : Y = 9.607.578
3. MATERIAL SPECIFICATION
   -LEVELING CONCRETE fc' = 10 MPa (CEMENT TYPE-I)
   -CONCRETE STRUCTURE fc' = 28 MPa (CEMENT TYPE-I)
   -DEFORMED BAR SNI 07-2052-2002, BJTP 40
   MINIMUM YIELD STRENGTH 4000 Kg/cm?
   -PLAIN BAR SNI 07-2052-2002, BJTP 24
   MINIMUM YIELD STRENGTH 2400 Kg/cm?
   -WIREMESH SHALL CONFORM TO ASTM A185 MIN. fy = 5000 Kg/cm?
   -GROUTING : NON SHRINK GROUT, COMP.
   STRENGTH = 35 MPA CONFORM TO ASTM C1107

PIPE SUPPORT & PIPE SLEEPER LIST

NO.	SUPPORT NO.	FDN TYPE	QTY	ELEV. TOC (mm)		INSERT PLATE			PEDESTAL		FOUNDATION		
						I? SIZE		I? TYPE	PEDESTAL SIZE		FDN SIZE		
				H1	H2	R	Q	–	X	Y	P	L	L1
1	SL-01-001 ~ 011	TYPE – 1	11	500	500	400	400	1	500	500	1000	1000	1700
2	SL-02-001 ~ 009	TYPE – 1	9	500	500	400	400	1	500	500	1000	1000	2650
3	SL-03-001 ~ 016	TYPE – 1	16	500	500	400	400	1	500	500	1000	1000	2650
4	SL-04-001 ~ 009	TYPE – 1	9	500	500	400	400	1	500	500	1000	1000	2400
5	SL-05-001 ~ 027	TYPE – 2	27	500	500	3500	300	2	400	3600	3600	1000	–
6	SL-06-001 ~ 010	TYPE – 2	10	500	500	2800	300	2	400	2900	2900	1000	–
7	SL-07-001 ~ 015	TYPE – 2	15	500	500	2800	300	2	400	2900	2900	1000	–
8	PRODUCTION FACILITY (PS23-001~043)	TYPE – 3	43	500	500	400	400	3	500	500	–	–	–
9	PRODUCTION FACILITY (PS26-001~005)	TYPE – 4	5	500	500	400	400	3	500	500	1000	1000	–
10	ST-103-01 ~ 07	TYPE – 4	7	500	500	400	400	3	500	500	1000	1000	–
11	ST-104-01 ~ 05	TYPE – 4	5	500	500	400	400	3	500	500	1000	1000	–
12	ST-105-01 ~ 02	TYPE – 4	2	500	500	400	400	3	500	500	1000	1000	–
13	ST-106-01 ~ 08	TYPE – 4	8	500	500	400	400	3	500	500	1000	1000	–
14	ST-106-01 ~ 08	TYPE – 4	8	500	500	400	400	3	500	500	1000	1000	–
15	PS23-0804-04 ~ 10	TYPE – 4	7	500	500	400	400	3	500	500	1000	1000	–
16	PS23-0804-04 ~ 10	TYPE – 4	7	500	500	400	400	3	500	500	1000	1000	–
17	ST-113-01 ~ 07	TYPE – 4	7	500	500	400	400	3	500	500	1000	1000	–
18	ST-114-01 ~ 10	TYPE – 4	10	500	500	400	400	3	500	500	1000	1000	–
19	ST-112-05 ~ 11	TYPE – 4	7	500	500	400	400	3	500	500	1000	1000	–
20	ST-112-20 ~ 23	TYPE – 4	4	500	500	400	400	3	500	500	1000	1000	
21	DRUM VESSEL (PS23-001~009)	TYPE – 3	9	500	500	400	400	3	500	500	–	–	

PIPE SLEEPER LAYOUT

SCALE 1 : 550

PIPE SUPPORT & PIPE SLEEPER LIST

NO.	SUPPORT NO.	FDN TYPE	QTY	ELEV. TOC (mm)		INSERT PLATE			PEDESTAL		FOUNDATION	
						I? SIZE		I? TYPE	PEDESTAL SIZE		FDN SIZE	
				H1	H2	R	Q	–	X	Y	P	L
22	NSF & WTIP (PS23-001~014)	TYPE – 3	14	500	500	400	400	3	500	500	–	–
23	TREATED WATER TANK (PS23-001~030)	TYPE – 3	30	500	500	400	400	3	500	500	–	–
24	ST-108-09 ~ 14	TYPE – 4	6	500	500	400	400	3	500	500	1000	1000
25	SUMP PIT (PS23-001~002)	TYPE – 3	2	500	500	400	400	3	500	500	–	–
26	WATER POND (PS23-001~004)	TYPE – 3	4	500	500	400	400	3	500	500	–	–
72	WATER POND (PS23-005~010)	TYPE – 4	6	500	500	400	400	3	500	500	–	–
28	ST-101-01 ~ 14	TYPE – 4	14	500	500	400	400	3	500	500	–	–
29	ST-101-01 ~ 08	TYPE – 4	8	500	500	400	400	3	500	500	–	–
30	ST-102-10 ~ 27 & ST-102-33 ~ 37	TYPE – 4	24	500	500	400	400	3	500	500	–	–
31	ST-111-01 ~ 14	TYPE – 4	14	500	500	400	400	3	500	500	–	–

*. FOUNDATION DETAIL SEE DWG. NO. TMBP-01-CS-DET-106

NOTES :

1. BEFORE STARTING CONSTRUCTION, CONTRACTOR SHALL VERIFY ACTUAL FIELD CONDITION AND DETERMINE LOCATION, ELEVATION OF EXISTING GRADING AND OTHER STRUCTURE. THE CONTRACTOR SHALL TAKE NECESSARY MEASURES TO HOLD SAFE AND PREVENT DAMAGE TO ANY EXISTING FACILITIES.

DRAWING REFERENCE	DESCRIPTION	REV	DATE	DESCRIPTION	PREPR'D	CHECK'D	APRV'D	CHECKED	APPROVED
TMBP-SP001-PI-LAY-D101~D117	PIPING LAYOUT AROUND								
TMBP-SP001-CS-LAY-D101	OVERALL PILE LAYOUT								
TMBP-SP001-PI-PLP-D101	OVERALL PLOT PLAN DRAWING	A	12-01-2026	ISSUED FOR REVIEW	NAS	AS	MR	YR	MRZ/RS

PT. PERTAMINA EP APPROVAL

PROCET :
JASA PEMBANGUNAN FASILITAS PRODUKSI STASIUN PENGUMPUL (SP) TANJUNG MIRING BARAT & KARANGAN TIMUR

OWNER : skkmigas PERTAMINA EP

CONTRACTOR : POG

SCALE : 1 : 550

DRAWING NO. TMBP-SP001-CS-FDN-D115

SHEET. NO. 1 OF 1

REV A

DRAWING TITLE :

FOUNDATION PLAN OF PIPE SLEEPER