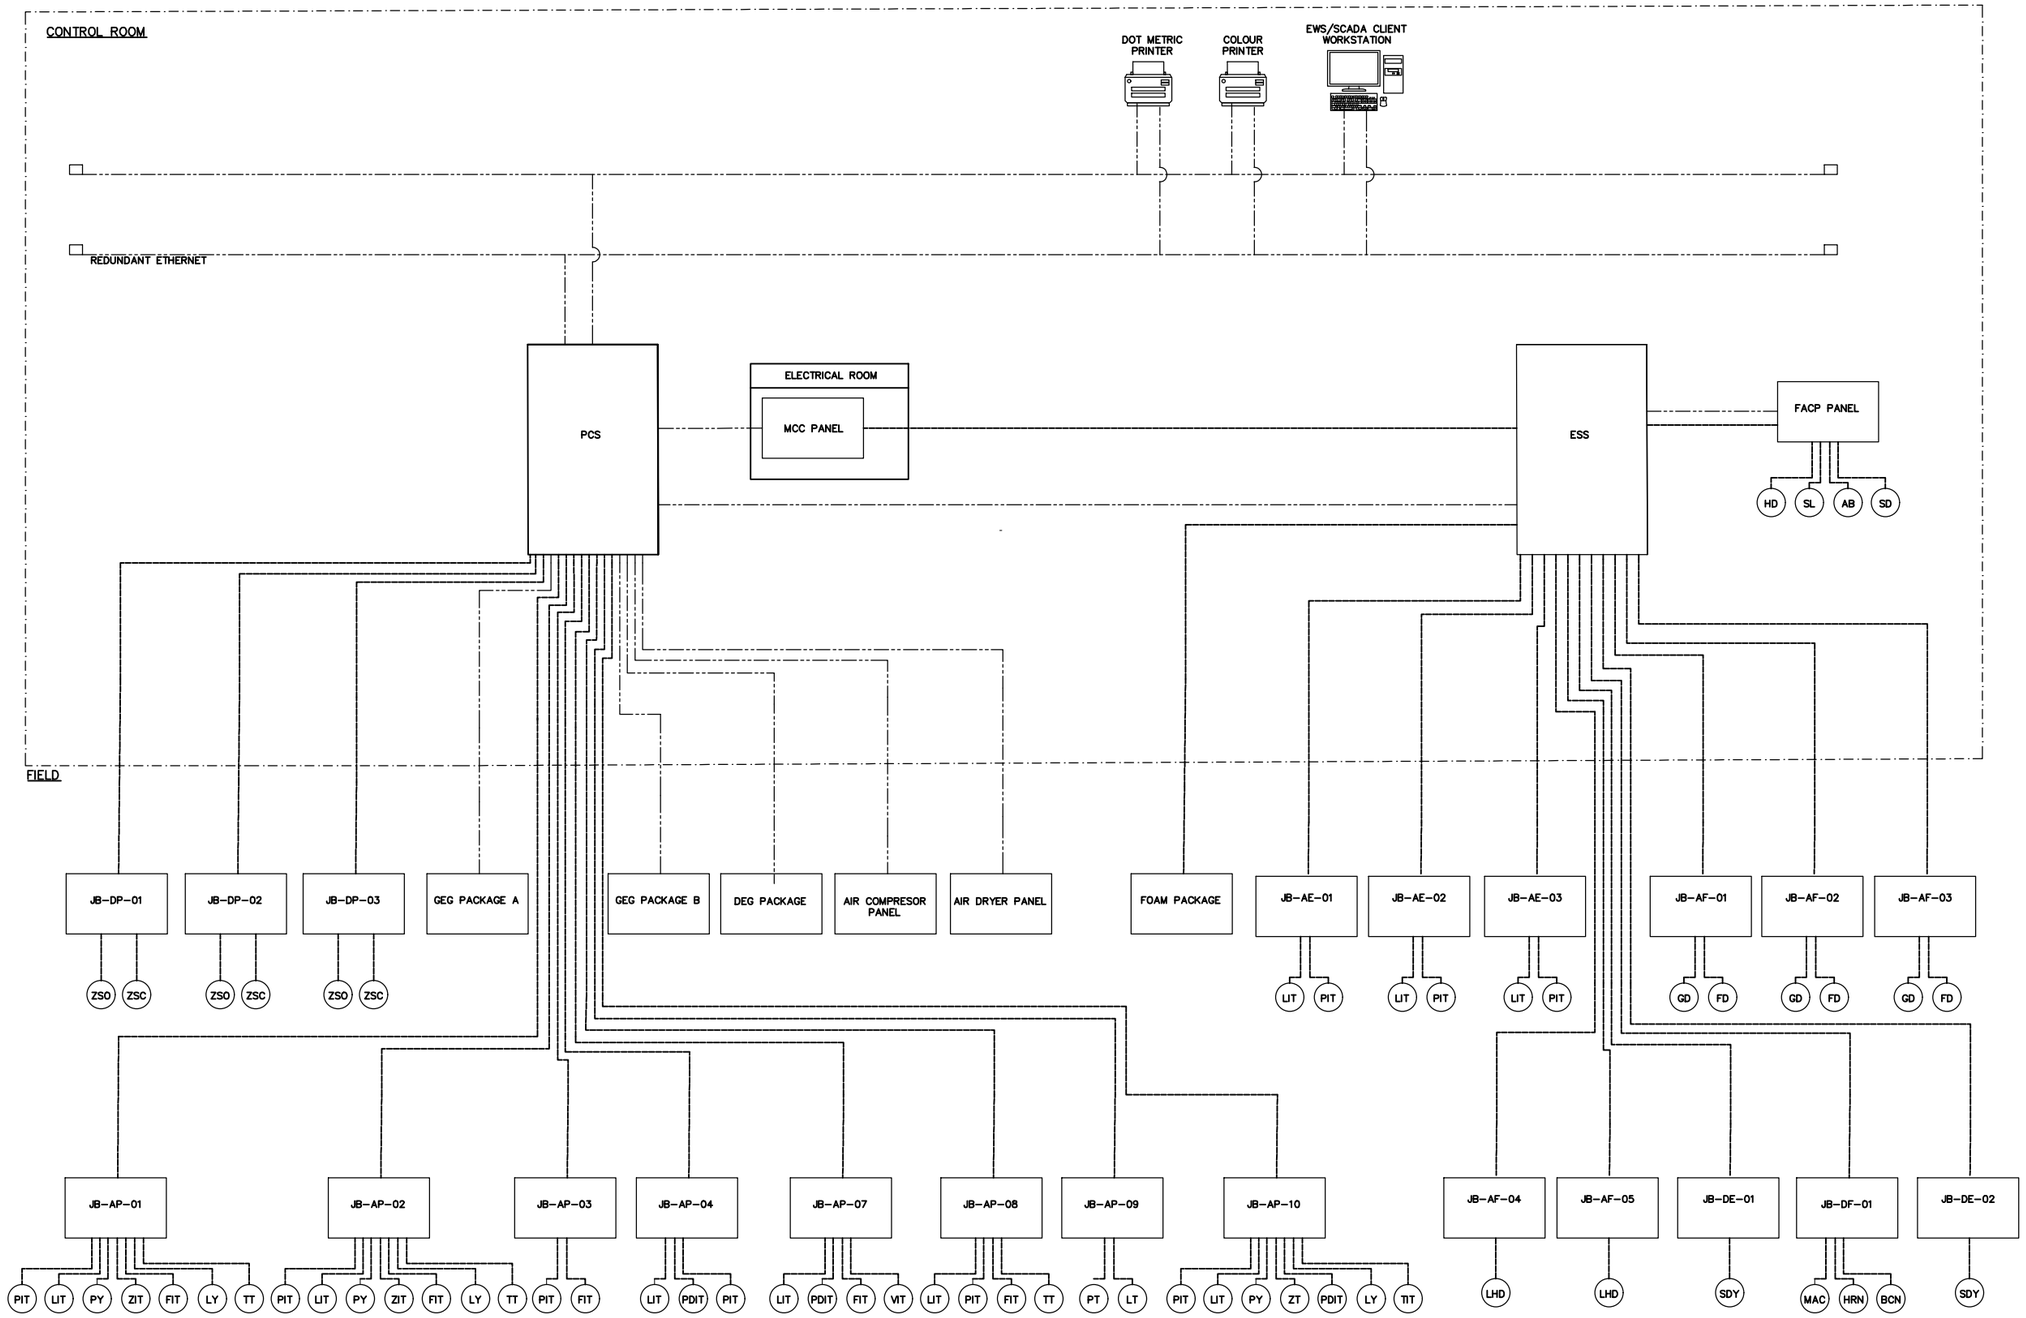

LEGEND

SDY	SOLENOID VALVE
BCN	BEACON
HRN	HORN
MAC	MANUAL ALARM CALL POINT
HD	LINEAR HEAT DETECTOR
GD	GAS DETECTOR
PIT	PRESSURE INDICATOR TRANSMITTER
LIT	LEVEL INDICATOR TRANSMITTER
FD	FLAME DETECTOR
PY	I/P POSITIONER
ZIT	POSITION INDICATOR TRANSMITTER
LY	I/P POSITIONER
TT	TEMPERATURE TRANSMITTER
PDIT	DIFFERENTIAL PRESSURE INDICATOR TRANSMITTER
VIT	VIBRATION INDICATOR TRANSMITTER
ZSO	OPEN POSITION SWITCH
ZSC	CLOSE POSITION SWITCH
ZT	POSITION TRANSMITTER
----------	HARDWIRED
----------	COMMUNICATION LINK (TCP/IP)
----------	COMMUNICATION LINK (RS-232)
----------	COMMUNICATION LINK (RS-485)
----------	COMMUNICATION LINK (ETHERNET)
SIS	: SAFETY INSTRUMENTED SYSTEM
PCS	: PROCESS CONTROL SYSTEM
FACP	: FIRE ALARM CONTROL PANEL
EWS	: ENGINEERING WORKSTATION
SCADA	: SUPERVISORY CONTROL AND DATA ACQUISITION
DEG	: DIESEL ENGINE GENERATOR
GEG	: GAS ENGINE GENERATOR
JB-DP	: JUNCTION BOX DIGITAL PROCESS
JB-AP	: JUNCTION BOX ANALOG PROCESS
JB-AF	: JUNCTION BOX ANALOG FGS
JB-DF	: JUNCTION BOX DIGITAL FGS
JB-AE	: JUNCTION BOX ANALOG SAFETY
JB-DE	: JUNCTION BOX DIGITAL SAFETY
MCC	: MOTOR CONTROL CENTER

NOTES :

DRAWING REFERENCE	DESCRIPTION	REV	DATE	DESCRIPTION	PREPR'D	CHECK'D	APRV'D	CHECKED	APPROVED
		A	31/12/2025	ISSUED FOR REVIEW	MHP	AS	RTN		

PT. PERTAMINA EP APPROVAL

PROCET :
JASA PEMBANGUNAN FASILITAS PRODUKSI STASIUN PENGUMPUL (SP) TANJUNG MIRING BARAT & KARANGAN TIMUR

OWNER : skkmigas PERTAMINA EP

CONTRACTOR : POG

SCALE : NTS

DRAWING NO. TMBP – SP001 – IN – BKD – D101

SHEET. NO. 1 OF 1

REV A

DRAWING TITLE :
SYSTEM CONTROL ARCHITECTURE BLOCK DIAGRAM