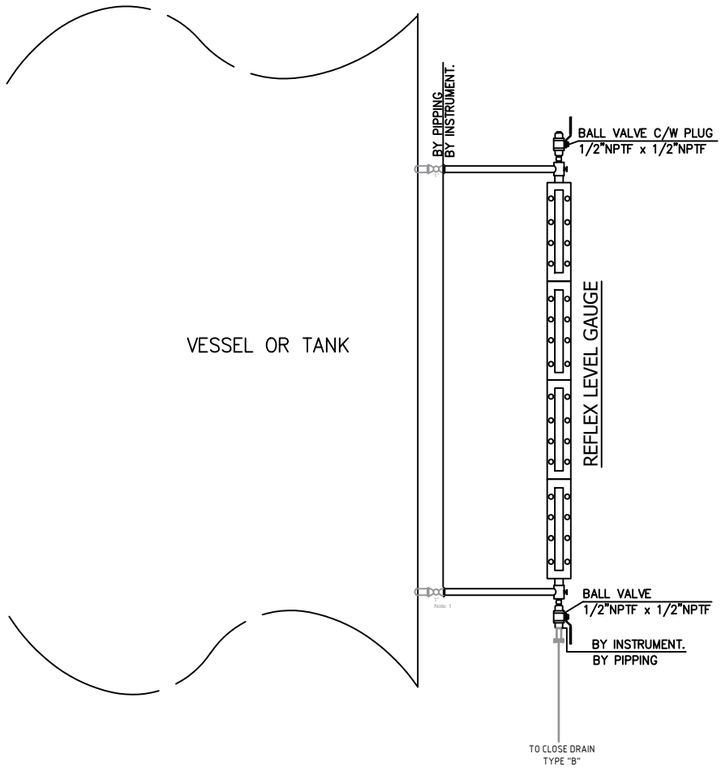

LIST FIELD INSTRUMENT

NO.	TAG. NO.	SERVICE	PROCESS PIPING / EQUIPMENT		STREAM TRACE	P & ID NO.
			CLASS	SIZE		
1	LG-V003-001	TEST SEPARATOR TMB	150#	1"	-	TMBP-01-PR-PID-101
2	LG-V002-001	PRODUCTION SEPARATOR KRG	150#	1"	-	TMBP-01-PR-PID-102
3	LG-V004-001	TEST SEPARATOR KRG	150#	1"	-	TMBP-01-PR-PID-102
4	LG-V005-001	PRODUCTION SCRUBBER	150#	1"	-	TMBP-01-PR-PID-114
5	LG-V006-001	KNOCK OUT DRUM VESSEL	150#	2"	-	TMBP-01-PR-PID-115
6	LG-V007-001	CLOSED DRAIN VESSEL	150#	2"	-	TMBP-01-PR-PID-116
7	LG-T017-001	POTABLE WATER TANK	150#	2"	-	TMBP-01-PR-PID-121
8	LG-V019-001	DIESEL STORAGE TANK	150#	2"	-	TMBP-01-PR-PID-122

NOTES :
1. GASKET, STUD BOLT & NUT SUPPLIED BY PIPING

DRAWING REFERENCE	DESCRIPTION	REV	DATE	DESCRIPTION	PREPR'D	CHECK'D	APRV'D	CHECKED	APPROVED
		A	30/12/2025	ISSUED FOR REVIEW	MHP	AS	RTN		

PT. PERTAMINA EP APPROVAL

PROJECT : JASA PEMBANGUNAN FASILITAS PRODUKSI STASIUN PENGUMPUL (SP) TANJUNG MIRING BARAT & KARANGAN TIMUR

OWNER : skkmigas PERTAMINA EP

CONTRACTOR : POG

SCALE : NTS

DRAWING NO. TMBP – SP001 – IN – HUP – D106

SHEET. NO. 1 OF 1

REV A

DRAWING TITLE : INSTRUMENT HOOK UP DIAGRAM LEVEL GAUGE – REFLEX TYPE