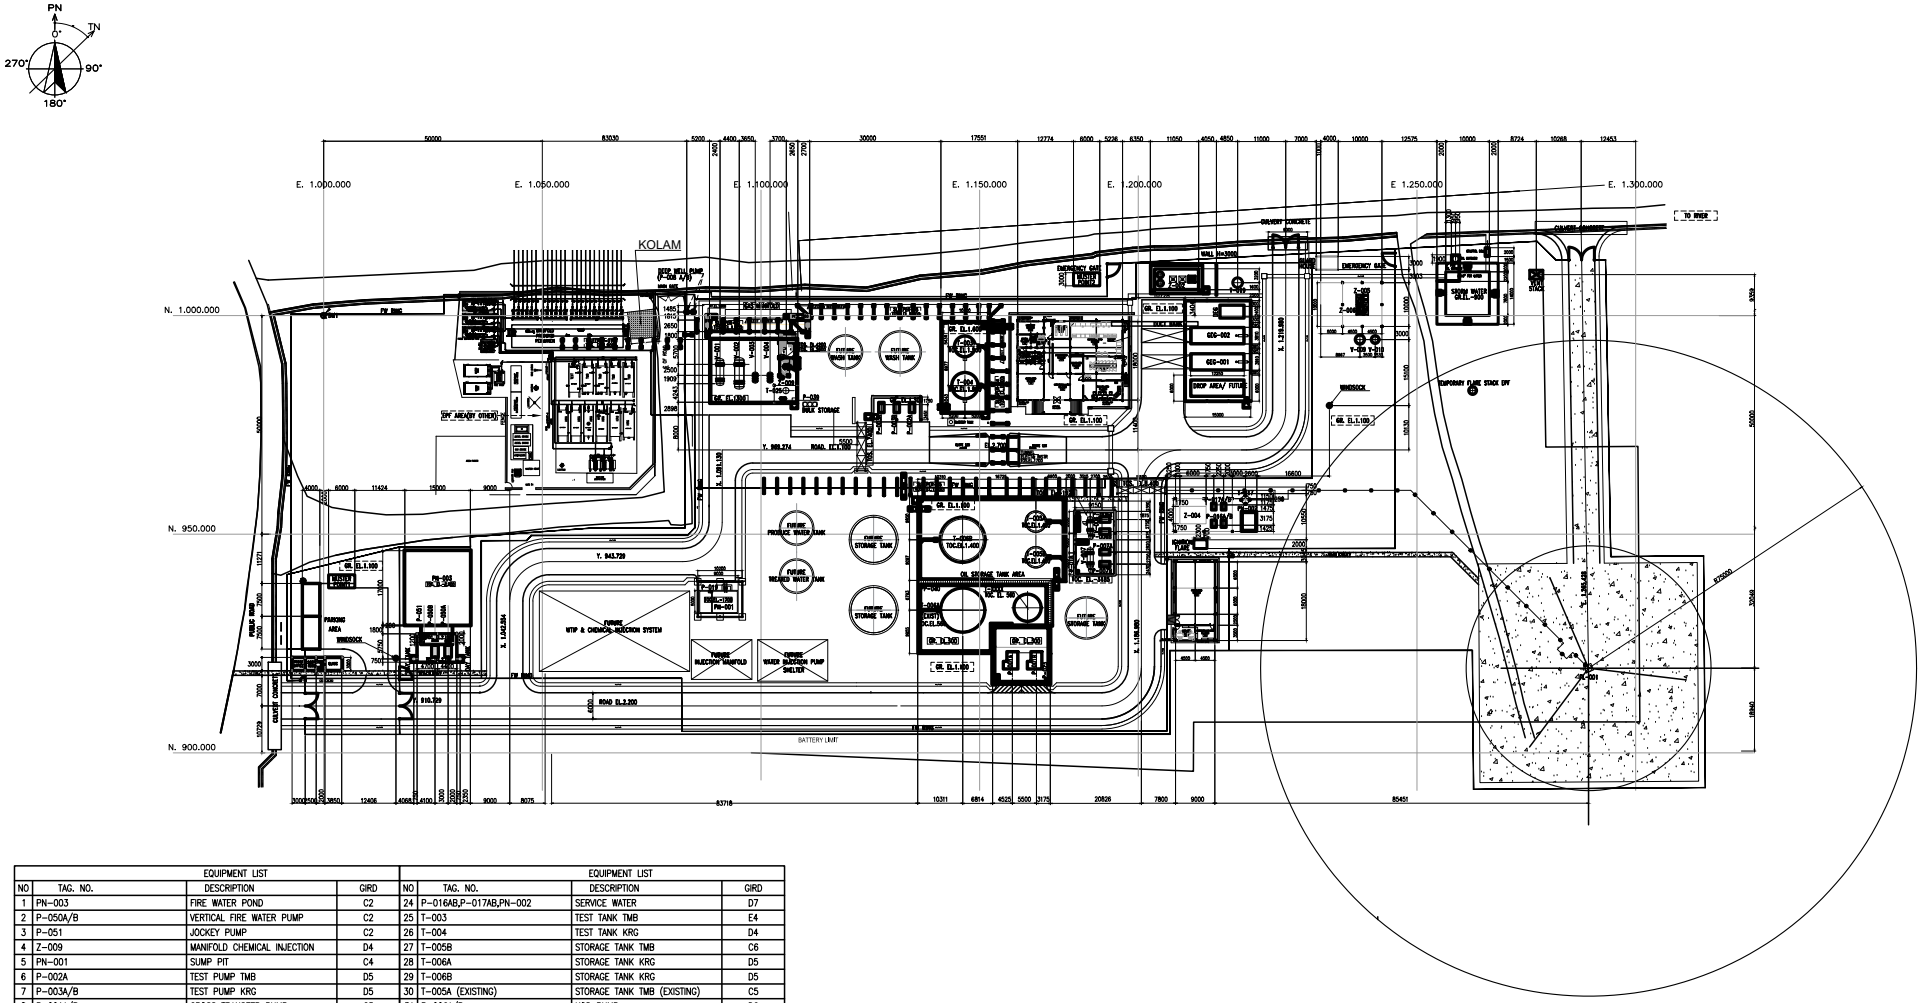
PN
TN
0°
270°
90°
180°
E. 1.000.000
E. 1.050.000
E. 1.100.000
E. 1.150.000
E. 1.200.000
E. 1.250.000
E. 1.300.000
N. 1.000.000
N. 950.000
N. 900.000
KOLAM
TO RIVER
BATTERY LIMIT
ROAD EL.3.200
WINDSOCK
PARKING AREA
EMPORARY FLARE STACK EPF
FUTURE WTP & CHEMICAL-INJECTION SYSTEM
FUTURE INJECTION MANIFOLD
FUTURE WATER INJECTION PUMP SHELTER
FUTURE PRODUCE WATER TANK
FUTURE INJECTED WATER TANK
FUTURE STORAGE TANK
OIL STORAGE TANK AREA
DROP AREA/ FUTUR
SNOW WATER CELL-SUP
EMERGENCY GAS
CULVERT CONCRETE
FW RING
PN-001
P-051
P-050A
P-050B
Z-009
Z-004
GEG-001
GEG-002
DEG-001
V-003
V-004
V-005
V-006
V-007
FL-001
T-003
T-004
T-005A
T-005B
T-006A
T-006B
T-017
T-019
P-016AB
P-017AB
P-018
P-019
P-021
P-023
P-002A
P-003A/B
P-001A/B
P-008A/B
P-007A/B
P-006A/B
P-016A/B
P-017A/B
P-002
V-001
V-002
Y. 943.720
Y. 909.374
X. 1.343.284
X. 1.376.989
X. 1.381.139
X. 1.376.989
X. 1.385.428
83030
83718
85451
50000
30000
17551
12774
12406
10311
6814
4525
5500
3170
20826
7800
9000
8075
4068
4100
3000
3850
3500
2500
2000
1500
1000
500
8724
10668
12453
10000
12575
11050
11000
7000
6350
5236
4400
3650
3700
2400
2700
2800
1485
1810
1900
2500
2586
1400
1500
1700
2000
2500
3500
4000
6000
11424
15000
9000
11171
10729
8000
7000
3000
1600
700
750
1150
1250
3175
1525
2500
10600
16000
18000
20000
30598
18898
8359
8000
6000
4000
2000
1000
500
2000
2000
2000